


Vaidehi Dhumal

Architectural Portfolio

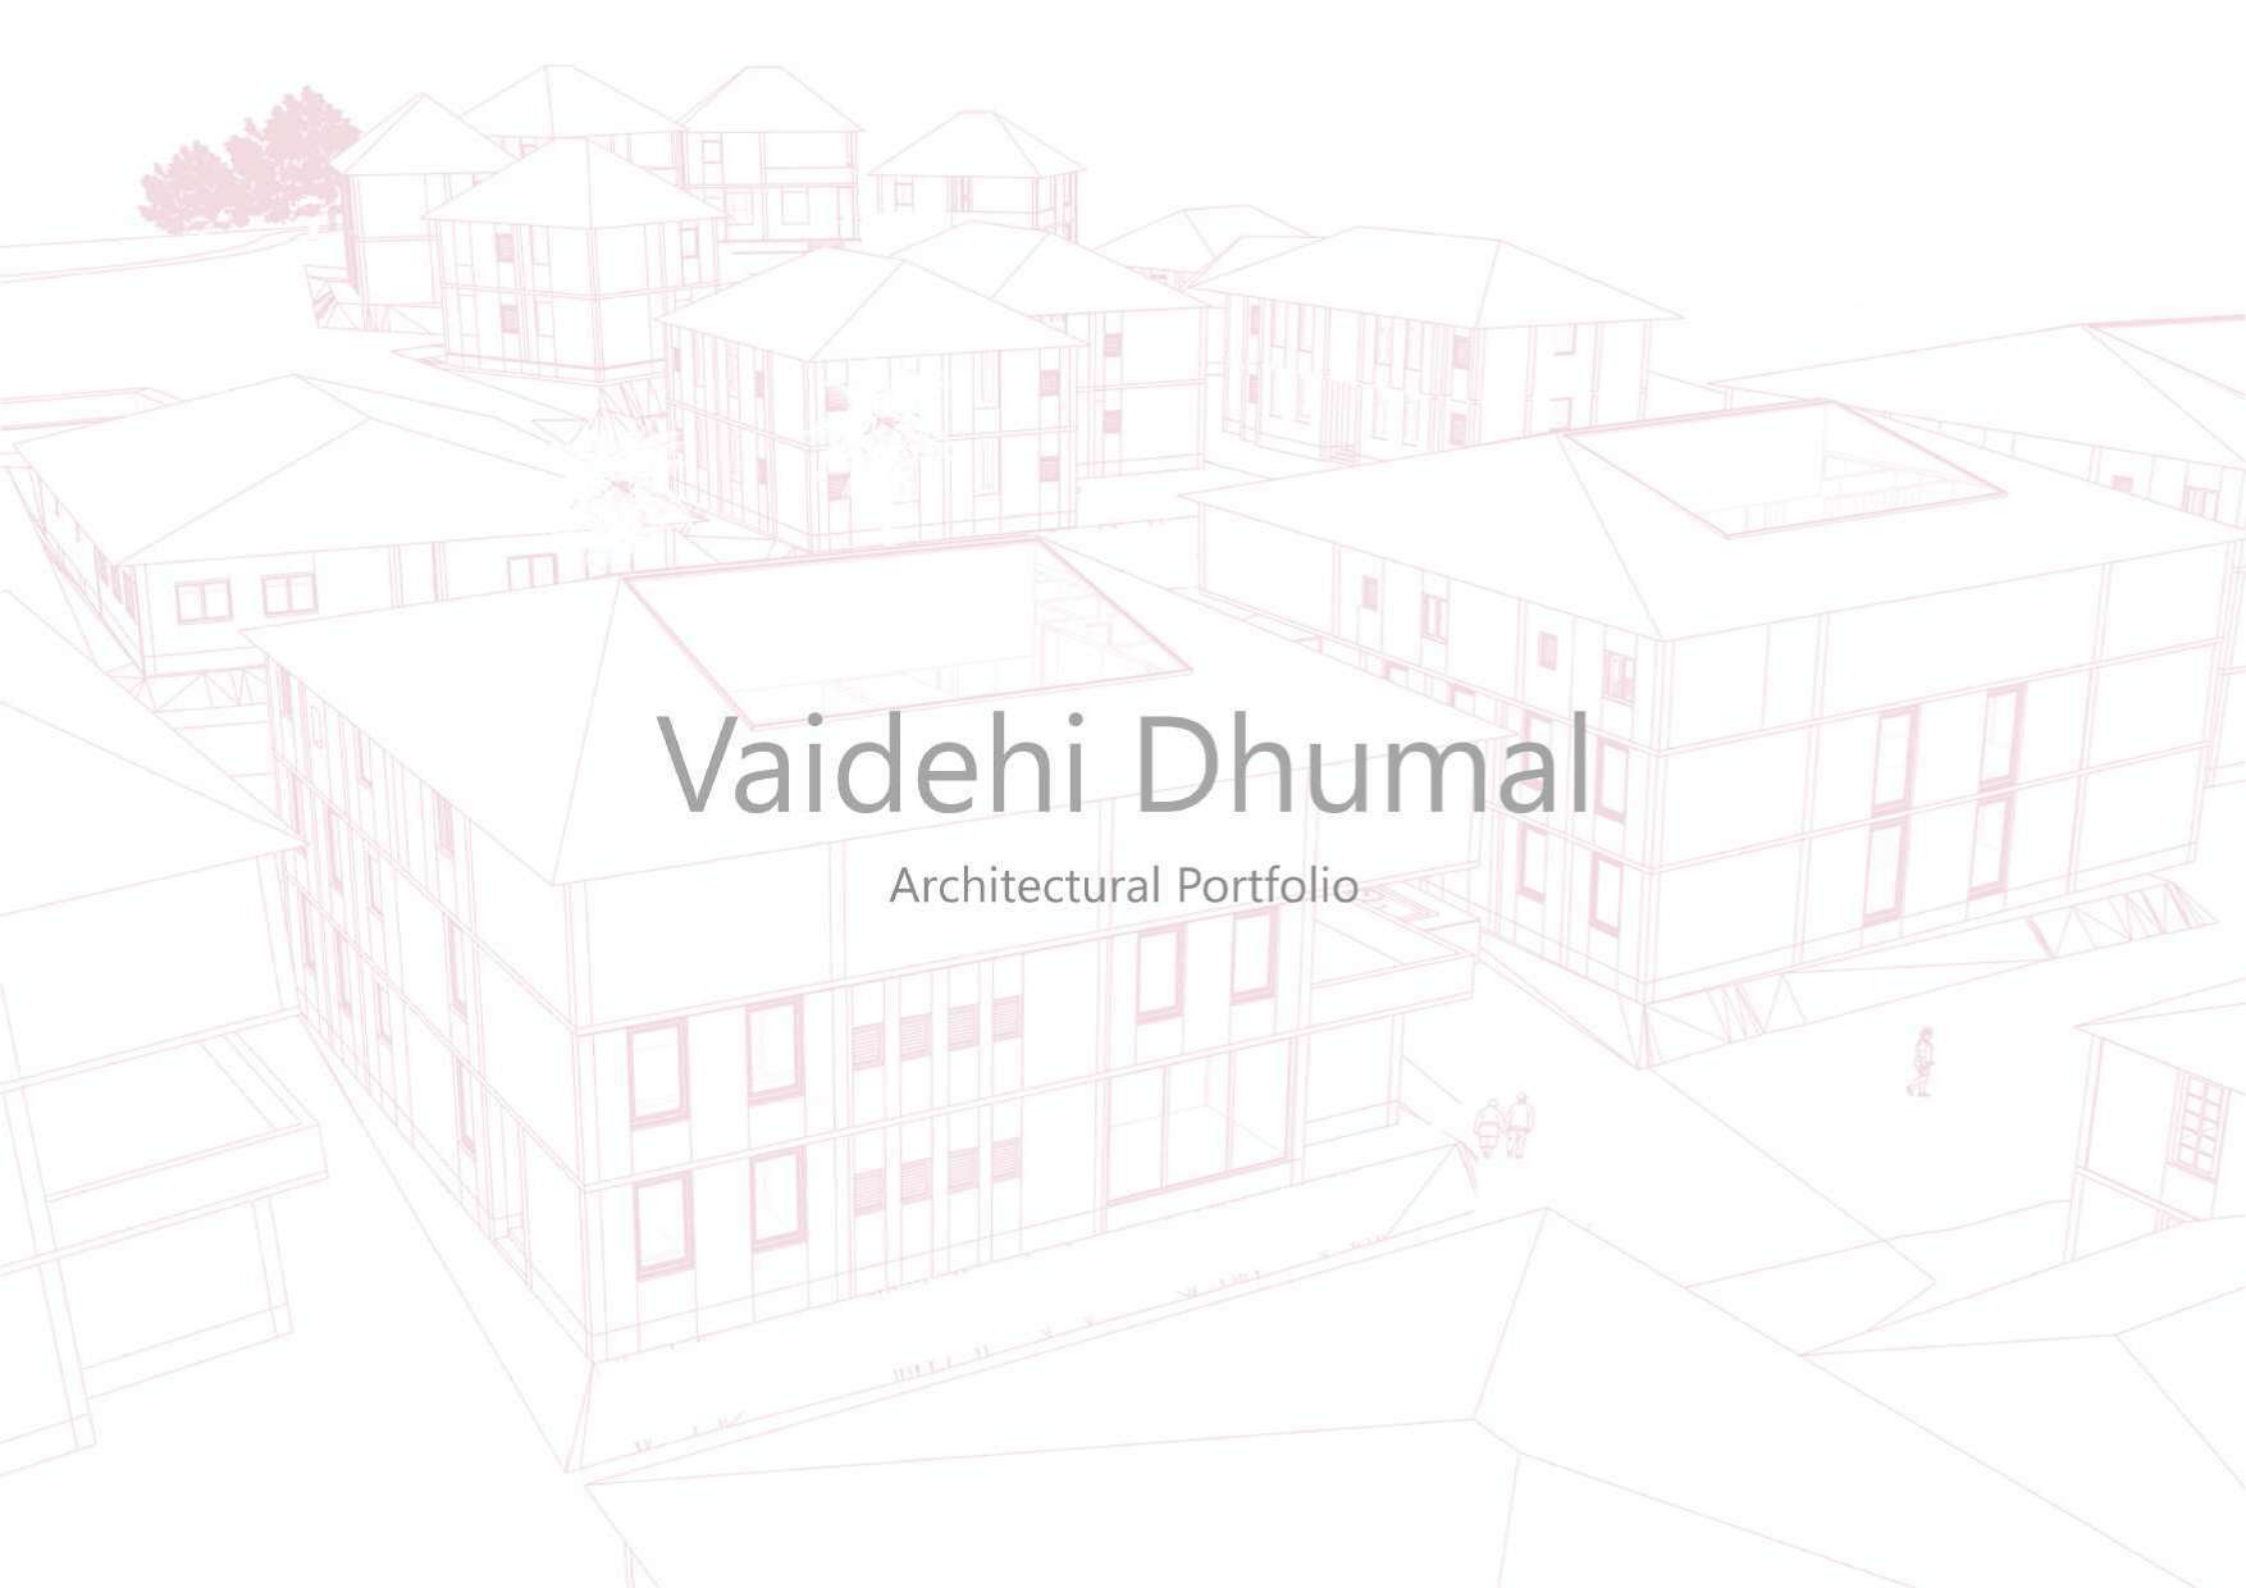

Thesis

VISAVA: A Resting Place

A wellness center located in the beautiful coastal region of Diveagar offers a serene escape from the stresses of daily life. Surrounded by breathtaking scenery, it provides a calming environment where guests can unwind through meditation, therapy sessions, and various holistic treatments. Alongside these, visitors can also participate in healthy recreational activities that promote both physical and mental well-being.

The idea behind the center is to help people relax, recover, and rejuvenate away from the hustle and bustle of city life.

Introduction

TOPIC INTRODUCTION

WELLNESS CENTRE:

A wellness center is a facility or establishment that focuses on promoting overall health, well-being, and balance—often by addressing physical, mental, emotional, and sometimes spiritual health. Wellness centers typically offer a variety of services, programs, and treatments aimed at helping individuals maintain or improve their quality of life. The specific offerings can vary widely depending on the focus of the center.

USERS

- General Public
- People with health needs
- Corporate Employ
- Senior Citizen
- People interested in different therapies
- Wellness Tourist

LOCATION

Diveagar is a serene village located in the Shrivardhan Taluka of Raigad district, Maharashtra,





Choosing Diveagar as a location for a wellness center is an excellent idea because of its unique attributes that align perfectly with the goals of health, relaxation, and rejuvenation.
Diveagar's pristine beach with golden sands and lush Casuarina trees offers a calm and tranquil setting, ideal for meditation, yoga, and relaxation.
Being a relatively less industrialized and populated area, the air quality is better, which can enhance the therapeutic experience.
The peaceful village atmosphere offers a slower pace of life, ideal for detox programs and stress-relief therapies.
Diveagar enjoys a tropical climate, with pleasant winters and refreshing monsoons, which are perfect for wellness activities like yoga, spa treatments, and outdoor therapy sessions.
Based on Diveagar's broader geography, this site could be part of a route connecting larger towns or tourist destinations like Diveagar Beach or other wellness-attracting zones, ensuring potential guest inflow.

ACCESSIBILITY

Diveagar is within driving distance from Mumbai (170 km) and Pune (160 km), making it a convenient destination for weekend getaways or short wellness retreats.
It is accessible via well-connected roads and scenic routes, which can add to the overall experience for visitors.

SITE BRIEF



Primary Road Secondary Road

The site is accessible by a road running along its boundary. This road connects to the village of Karle, The site is located immediately south of Karle village, which is likely a hub for local amenities. The proximity to the village ensures easy access for both staff and visitors.

Transportation

Public and Private Transport:

Private vehicles: Visitors may rely on personal cars or taxis

Public transport: Check if local buses or shared vehicles connect Karle to nearby cities or towns for staff and visitors without private transport.

Local Transport in Diveagar

•Auto-rickshaws and shared jeeps are the primary modes of transport within Diveagar and nearby areas.
•Bicycles or scooters can be rented for short-distance travel, ideal for exploring Diveagar beach and surrounding attractions.

Flora



Coconut Tree



Betel Nut tree



Mango Tree

Site Surroundings




Suvarna Ganesh Temple



Diveagar Beach (Approx. 2 km)

Sun path & Wind direction

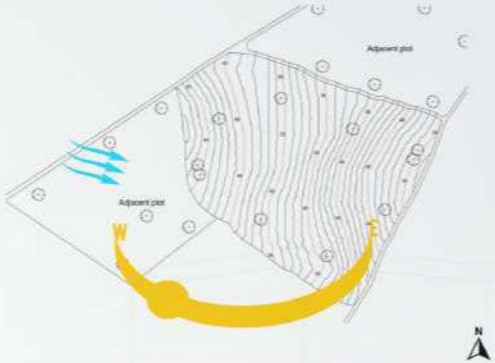











Views & vistas


Site Plan


LEGEND
1. ADMINISTRATION
2. HEALTHCARE CENTER
3. TREATMENT ROOMS (MALE)
4. TREATMENT ROOMS (FEMALE)
5. YOGA ROOM
6. CAFETERIA
7. SINGLE OCCUPANCY
8. DOULBE OCCUPANCY
9. DORMS
10. VILLA
11. CHANGING ROOMS
12. SWIMMING POOL
13. AMPHITHEATRE
14. BASKETBALL COURT
15. DIRECTOR'S ROOM
16. STAFF QUARTERS
17. PARKING
18 M WIDE ROAD
N

Admin & Healthcare

Admin
Area : 290 sq.m

Healthcare
Area : 310 sq.m

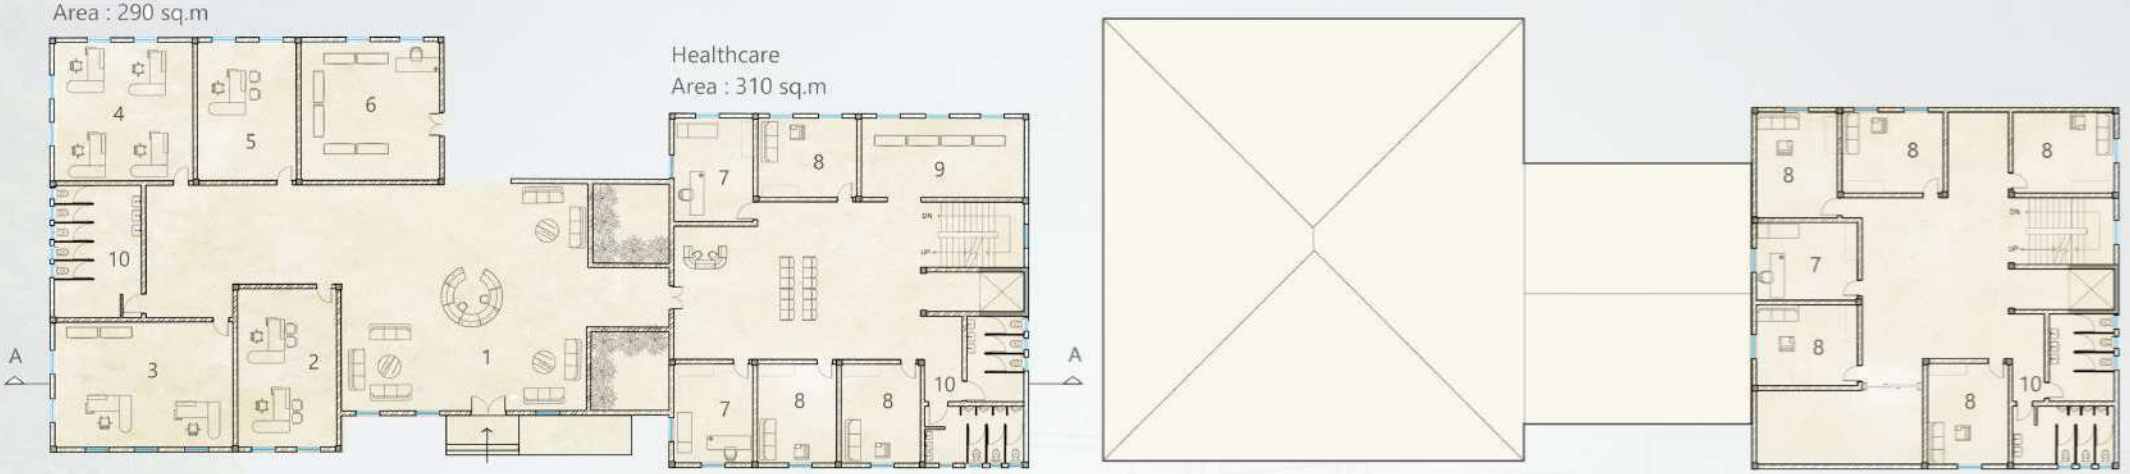

Legend

1. Reception & Waiting
2. Admin
3. Management and Records
4. Accounts
5. Director's Cabin
6. Souvenirs
7. Physician's Room
8. Therapist Room
9. Pathology Lab
10. Toilets
11. Staircase
12. Lift



Section AA


Admin & Healthcare




Treatment rooms : Female

Treatment Rooms Female
Area : 847 sq.m


Legend
1. Accupressure
2. Accupuncture
3. Pebble Pool
4. Hip Bath
5. Steam Bath
6. Spinal Bath
7. Hydro Therapy
8. Sauna
9. Cold circular jet
10. Enema
11. Toilet
12. Staircase
13. Lift
14. Courtyard
15. Changing Room
16. Physiotherapy
17. Mud Bath

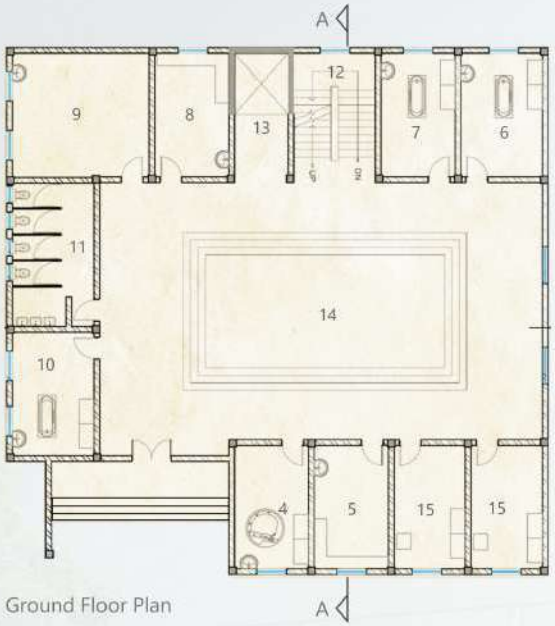


Ground Floor Plan

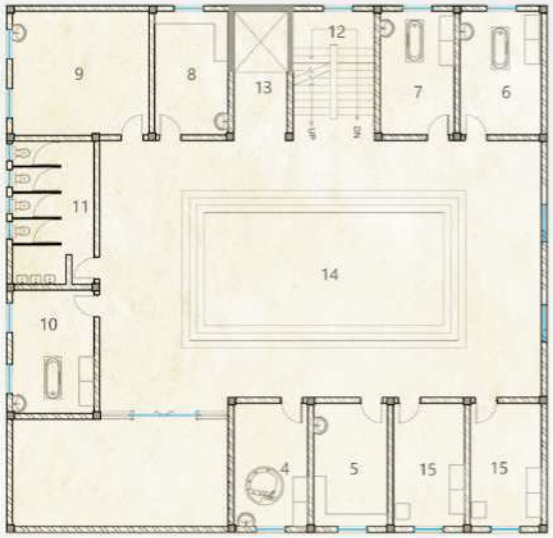


First Floor Plan

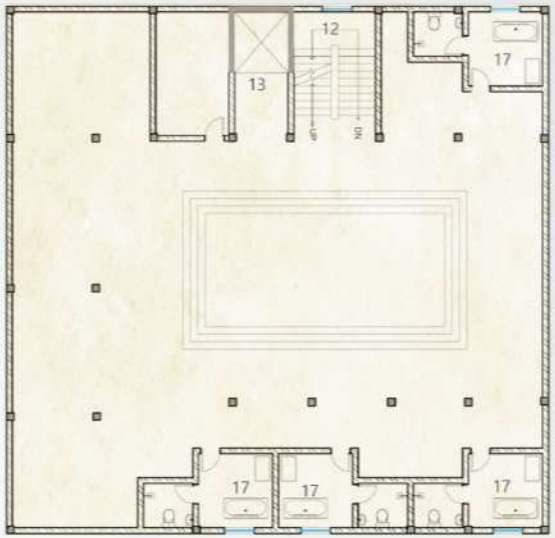


Second Floor Plan

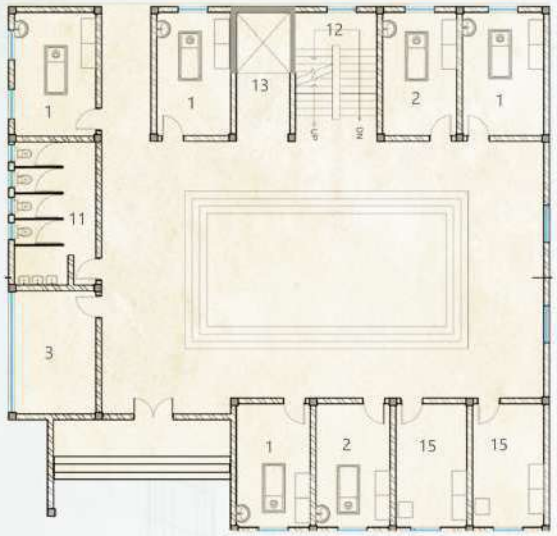

Ground Floor Plan

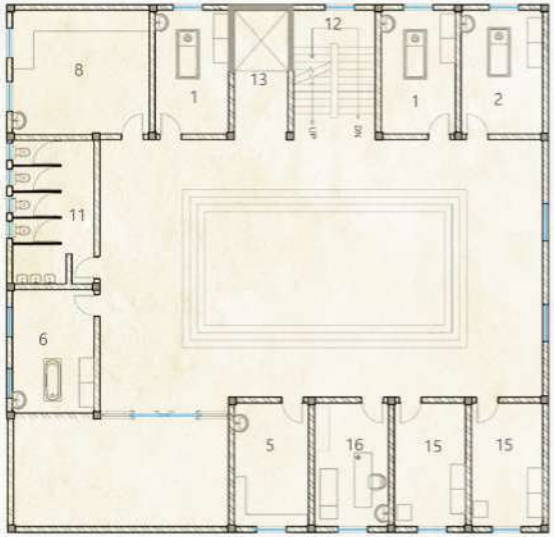


First Floor Plan

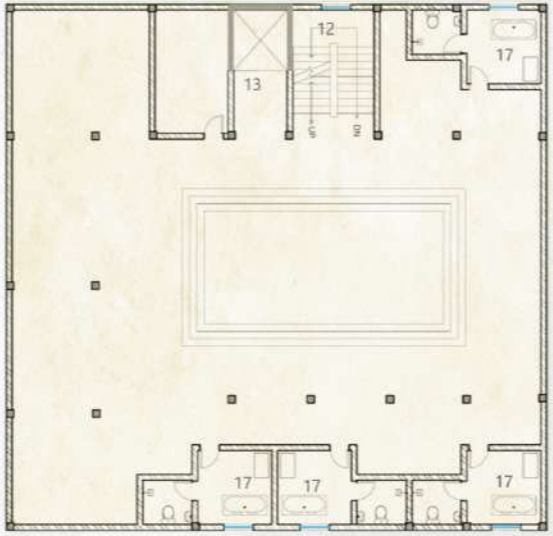


Second Floor Plan

Treatment rooms : Female

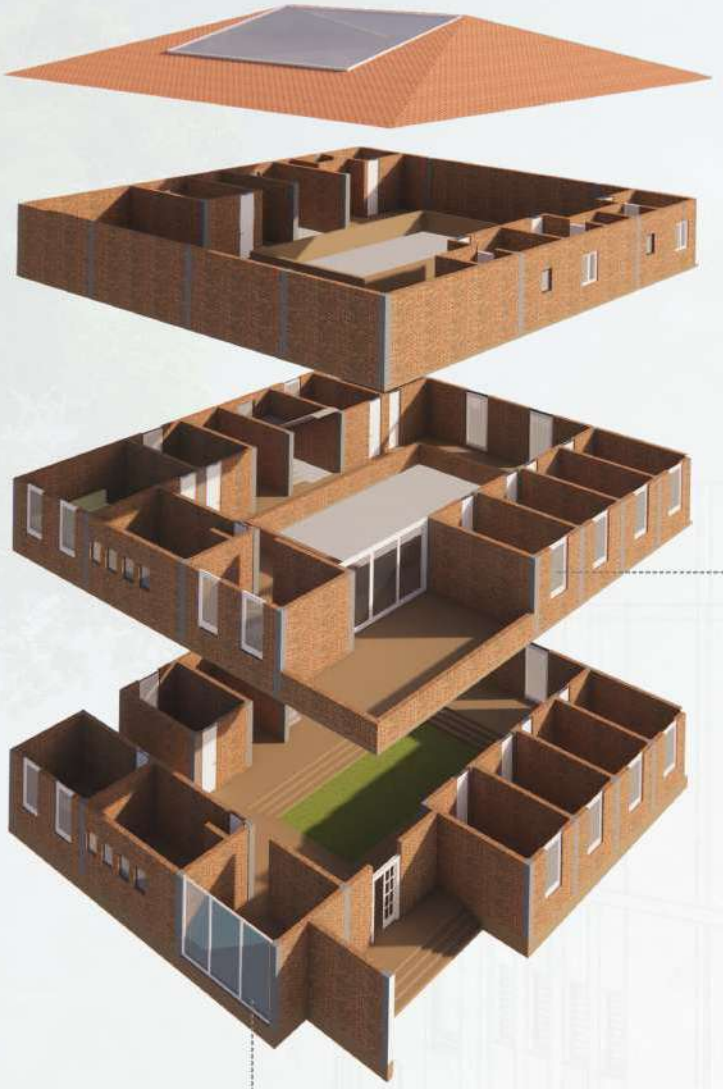

Axonometric View

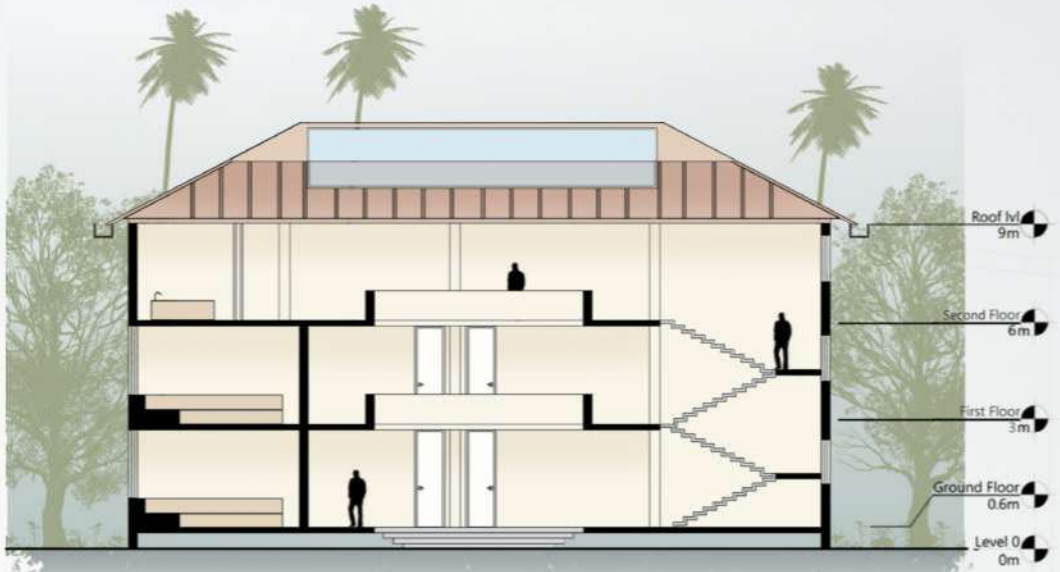

Section AA




Pebble Room




Physiotherphy Room

Treatment rooms : Male

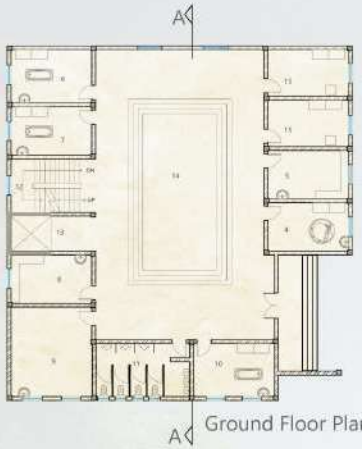


Ground Floor Plan

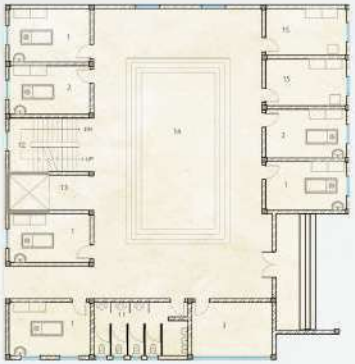


Ground Floor Plan


Treatment Rooms Male
Area : 847 sq.m

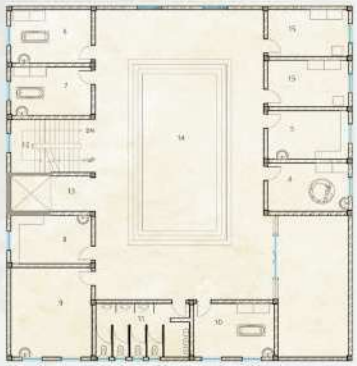


First Floor Plan

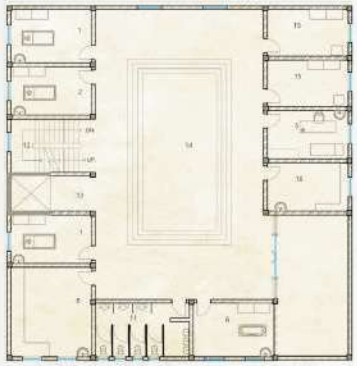

First Floor Plan

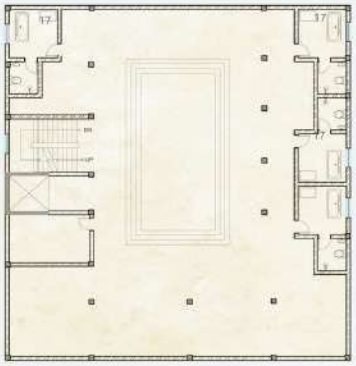

Second Floor Plan

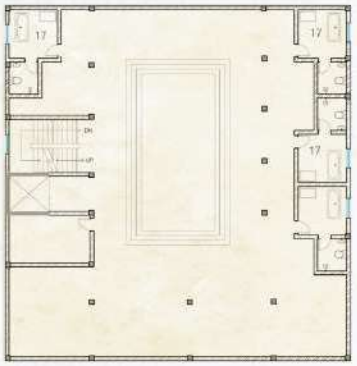

Second Floor Plan

Legend
1. Accupressure
2. Accupuncture
3. Pebble Pool
4. Hip Bath
5. Steam Bath
6. Spinal Bath
7. Hydro Therapy
8. Sauna
9. Cold circular jet
10. Enema
11. Toilet
12. Staircase
13. Lift
14. Courtyard
15. Changing Room
16. Physiotherapy
17. Mud Bath




Section AA



Front Elevation

Treatment rooms : Male



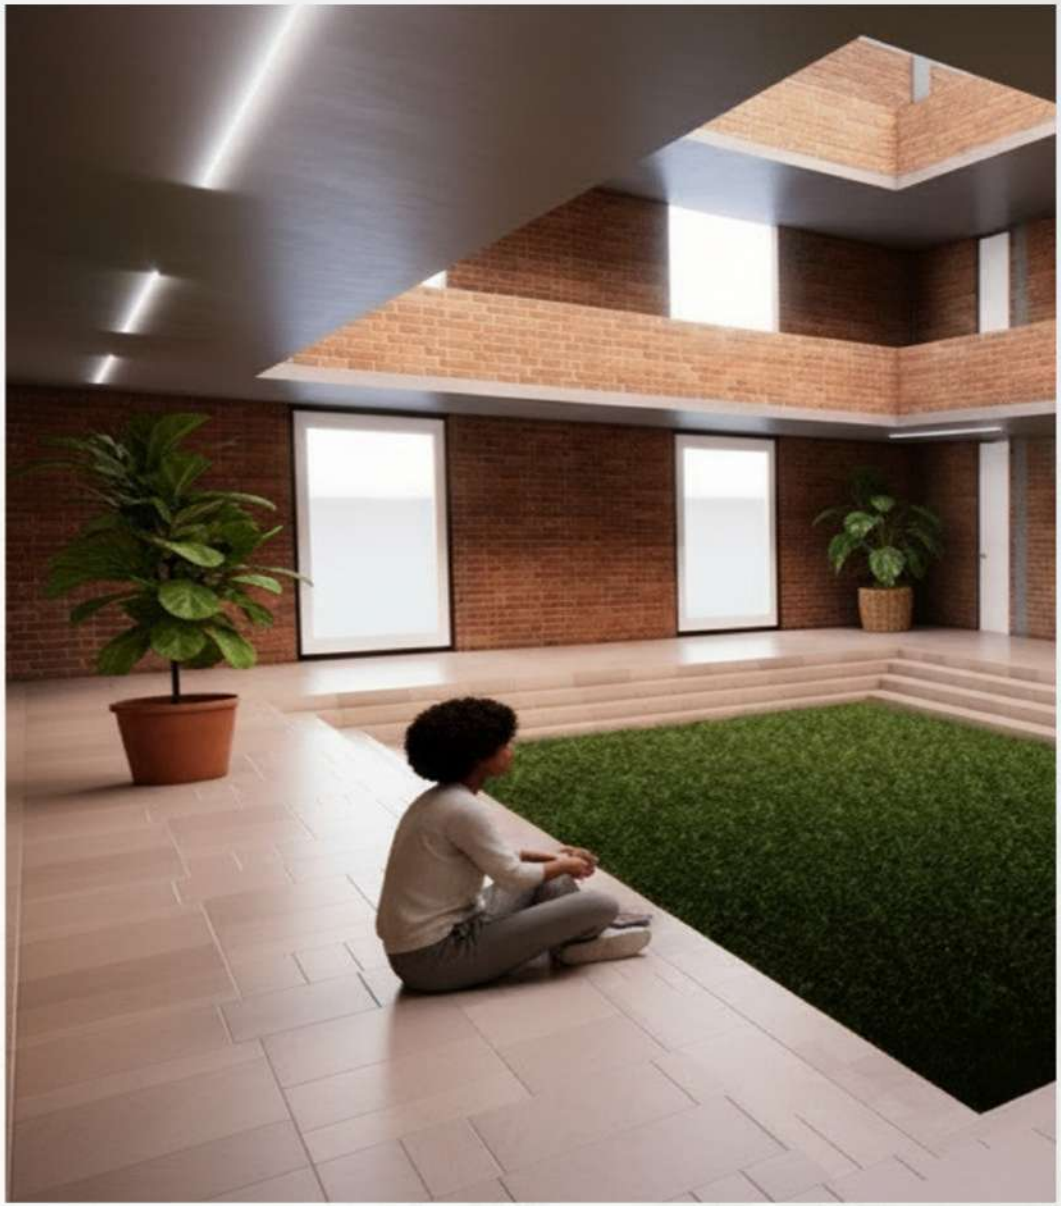

Single Occupancy

Single Occupancy Rooms
Area : 200 sq.m



Legend
1. Entrance
2. Bedroom
3. Toilet
4. Staircase

Ground Floor Plan



First Floor Plan



Section AA




Front Elevation

Single Occupancy




Double occupancy rooms

Double Occupancy Rooms
Area : 225 sq.m

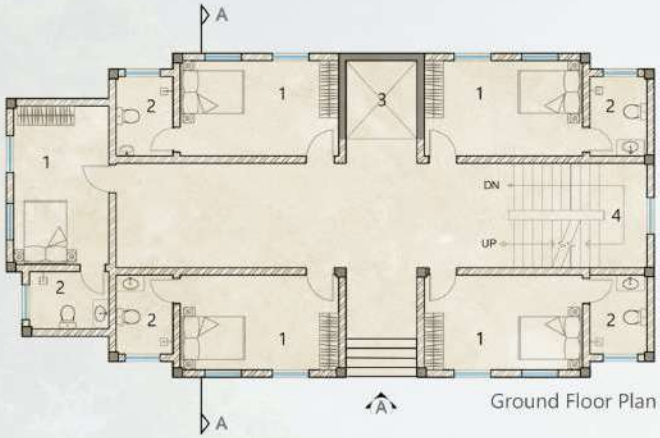

Ground Floor Plan

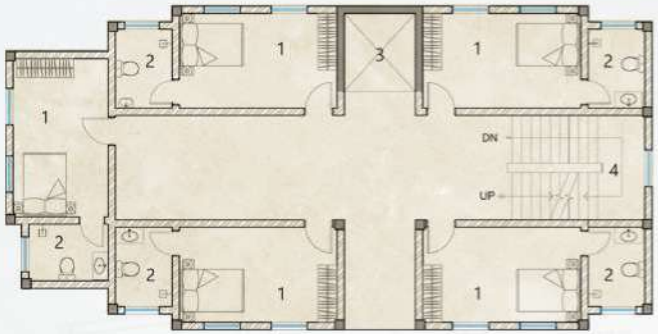

First Floor Plan

Legend

1. Room
2. Toilet
3. Lift
4. Stairs
5. Lobby



Axonometric View



Section AA




Elevation A



Interior View

Dorm rooms

Dormitory
Area : 150 sq.m

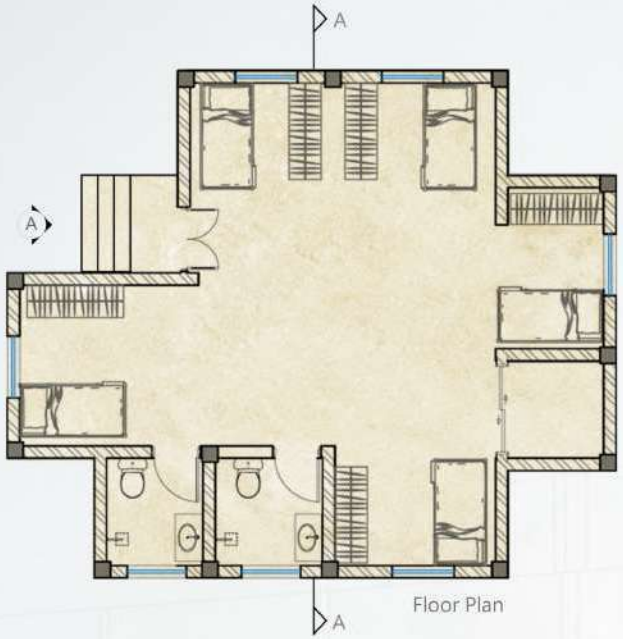

Floor Plan



Section A A


Interior View




Elevation A

Dorm Rooms



Dining Hall

Dining Hall
Area : 420 sqm

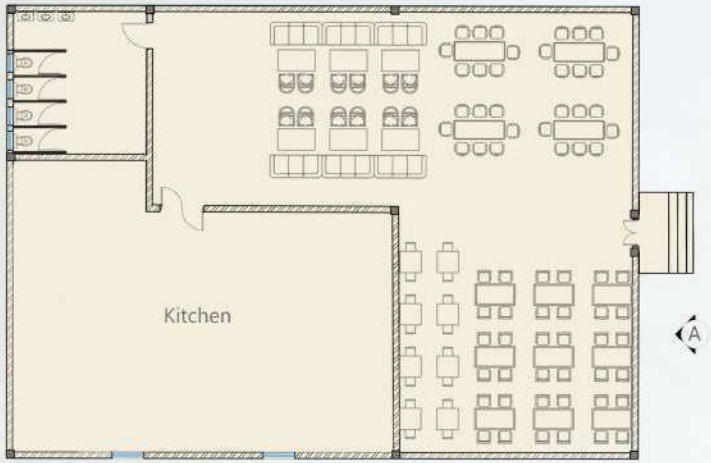

Ground floor plan



Exterior view




Elevation A




Interior view

Villa

Villa
Area : 60 sq.m

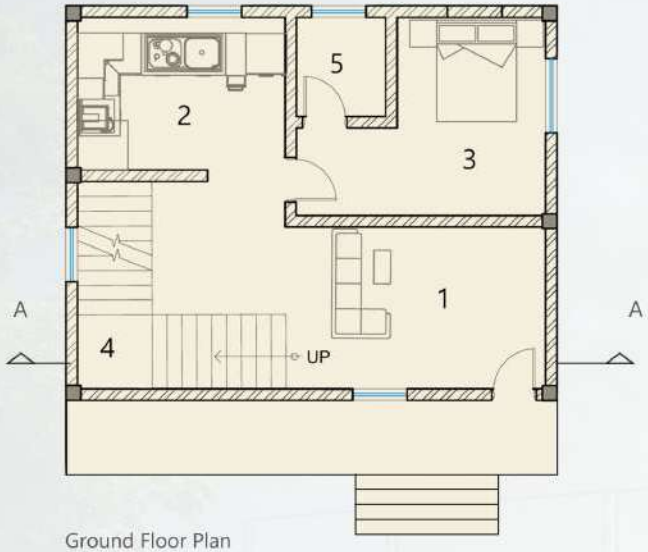

Ground Floor Plan

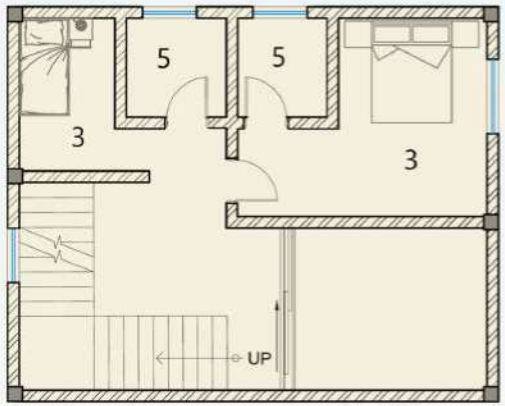

First Floor Plan

Legend
1. Hall
2. Kitchen
3. Bedroom
4. Toilet



Axonometric View



Section AA



Elevation A













Internship

During my internship, I worked on a variety of interior design projects that included furniture design, renovation work, and contour model making. The experience allowed me to understand different stages of the design process from conceptual development to detailed execution.


Railing Details

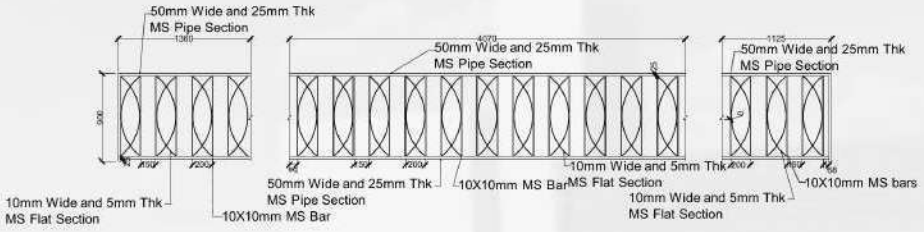

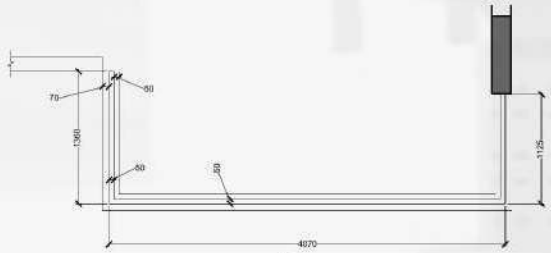

Plan

Railing on Second Floor Terrace

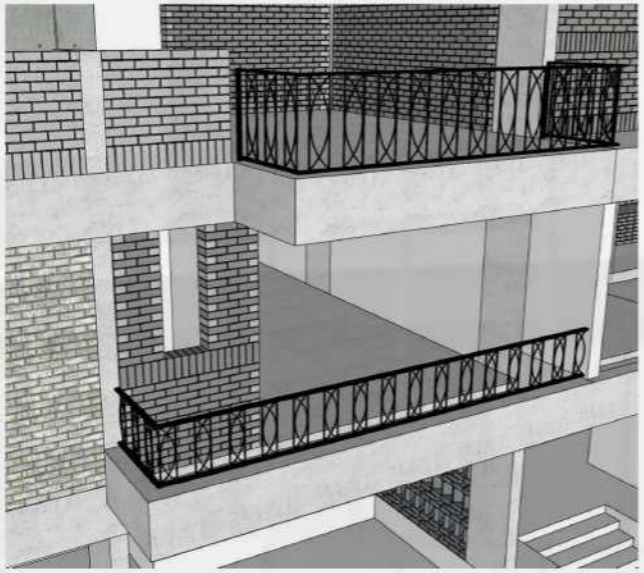











-ALL DIMENSIONS ARE IN MM
-ALL DIMENSIONS IN THE DRAWING ARE TO BE READ AND NOT TO BE MEASURED
-THIS DRAWING SHALL SUPERSEDE ITS PREVIOUS REVISIONS.
-ALL DIMENSIONS SHALL BE CO-RELATED WITH STRUCTURAL AND SERVICE DRAWINGS AND ANY AMBIGUITY SHALL BE IMMEDIATELY BROUGHT TO THE NOTICE OF THE ARCHITECT BEFORE THE COMMENCEMENT OF WORK.


Staircase Details

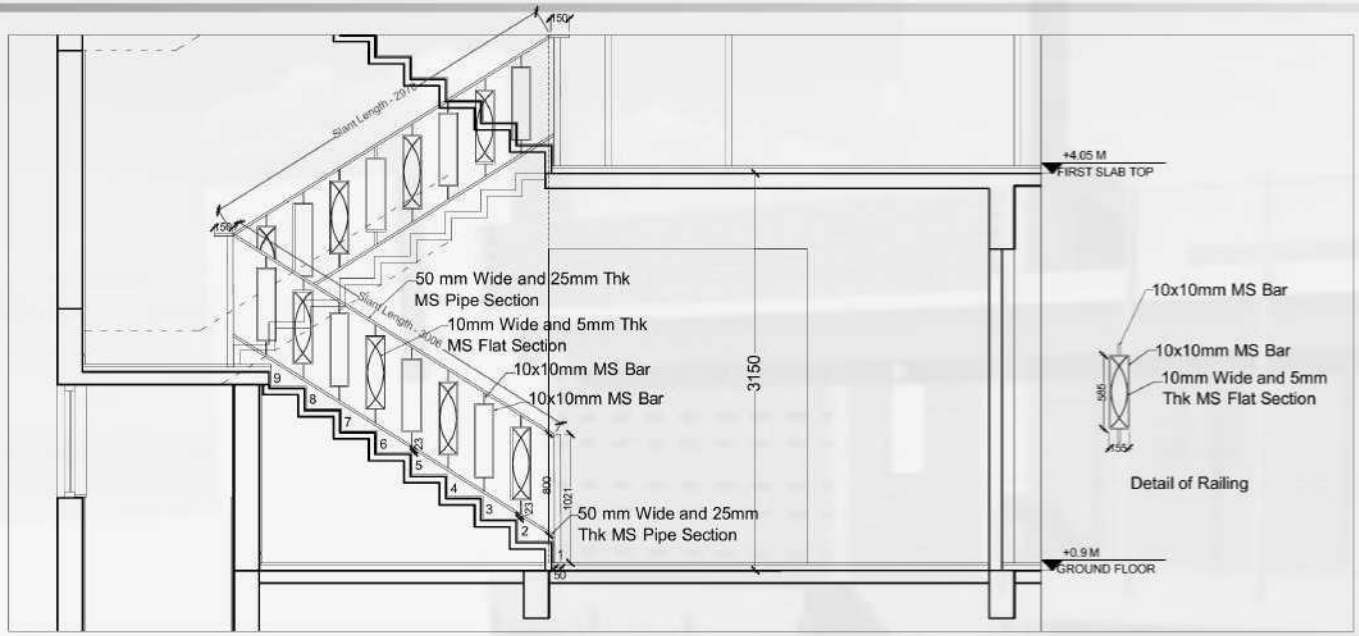

Detail of Railing

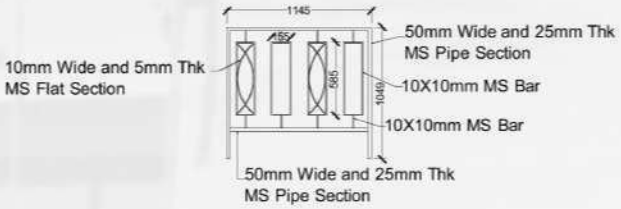

Staircase Railing
on Third Floor

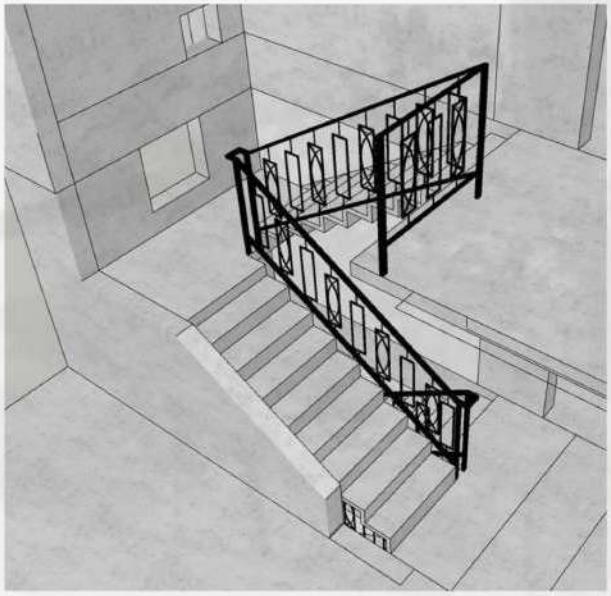







-ALL DIMENSIONS ARE IN MM
-ALL DIMENSIONS IN THE DRAWING ARE TO BE READ AND NOT TO BE MEASURED
-THIS DRAWING SHALL SUPERSEDE ITS PREVIOUS REVISIONS.
-ALL DIMENSIONS SHALL BE CO-RELATED WITH STRUCTURAL AND SERVICE DRAWINGS AND ANY AMBIGUITY SHALL BE IMMEDIATELY BROUGHT TO THE NOTICE OF THE ARCHITECT BEFORE THE COMMENCEMENT OF WORK.

Villa Elevation




-ALL DIMENSIONS ARE IN MM
-ALL DIMENSIONS IN THE DRAWING ARE TO BE READ AND NOT TO BE MEASURED
-THIS DRAWING SHALL SUPERSEDE ITS PREVIOUS REVISIONS.
-ALL DIMENSIONS SHALL BE CO-RELATED WITH STRUCTURAL AND SERVICE DRAWINGS AND ANY AMBIGUITY SHALL BE IMMEDIATELY BROUGHT TO THE NOTICE OF THE ARCHITECT BEFORE THE COMMENCEMENT OF WORK.

Kalashree Views




-ALL DIMENSIONS ARE IN MM
-ALL DIMENSIONS IN THE DRAWING ARE TO BE READ AND NOT TO BE MEASURED
-THIS DRAWING SHALL SUPERSEDE ITS PREVIOUS REVISIONS.
-ALL DIMENSIONS SHALL BE CO-RELATED WITH STRUCTURAL AND SERVICE DRAWINGS AND ANY AMBIGUITY SHALL BE IMMEDIATELY BROUGHT TO THE NOTICE OF THE ARCHITECT BEFORE THE COMMENCEMENT OF WORK.

Demolition Plan

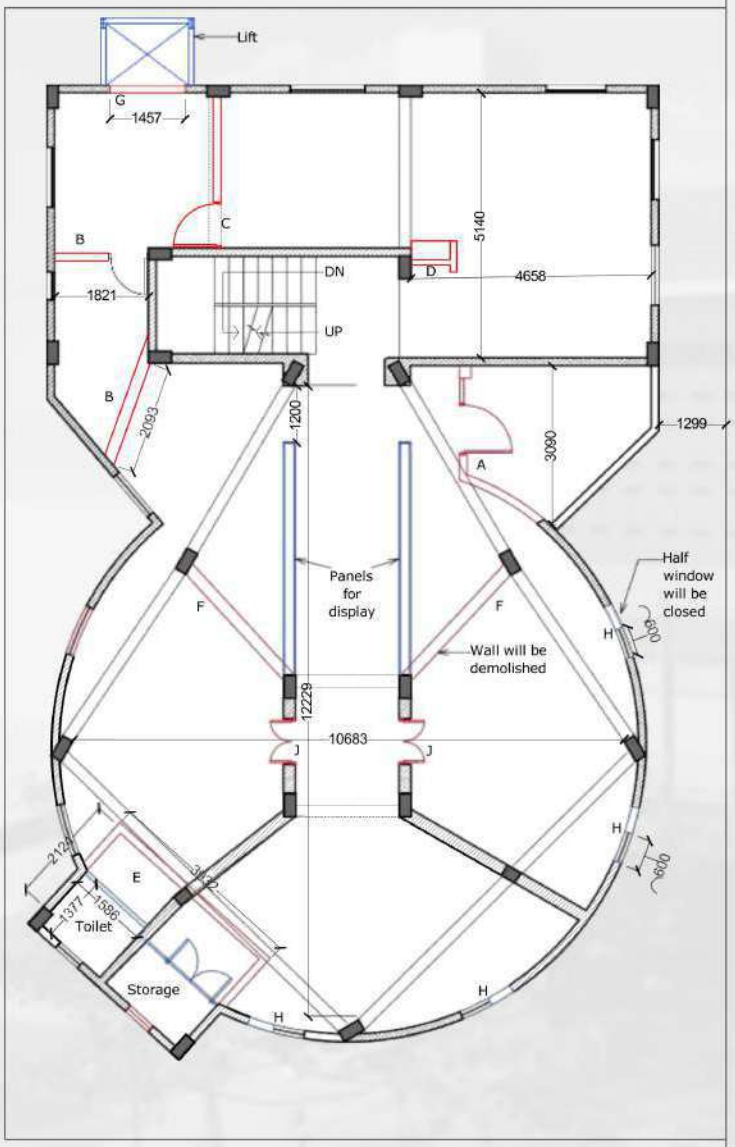


Second Floor Demolition Plan

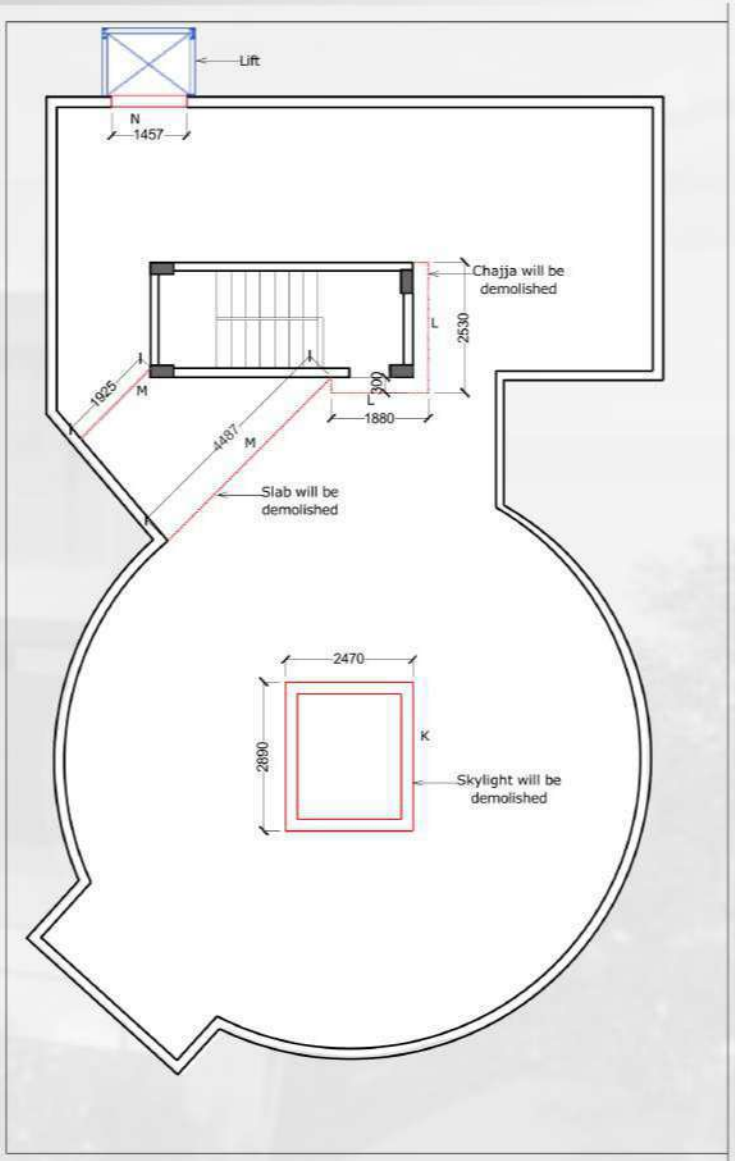


Terrace Demolition Plan

-ALL DIMENSIONS ARE IN MM
-ALL DIMENSIONS IN THE DRAWING ARE TO BE READ AND NOT TO BE MEASURED
-THIS DRAWING SHALL SUPERSEDE ITS PREVIOUS REVISIONS.
-ALL DIMENSIONS SHALL BE CO-RELATED WITH STRUCTURAL AND SERVICE DRAWINGS AND ANY AMBIGUITY SHALL BE IMMEDIATELY BROUGHT TO THE NOTICE OF THE ARCHITECT BEFORE THE COMMENCEMENT OF WORK.

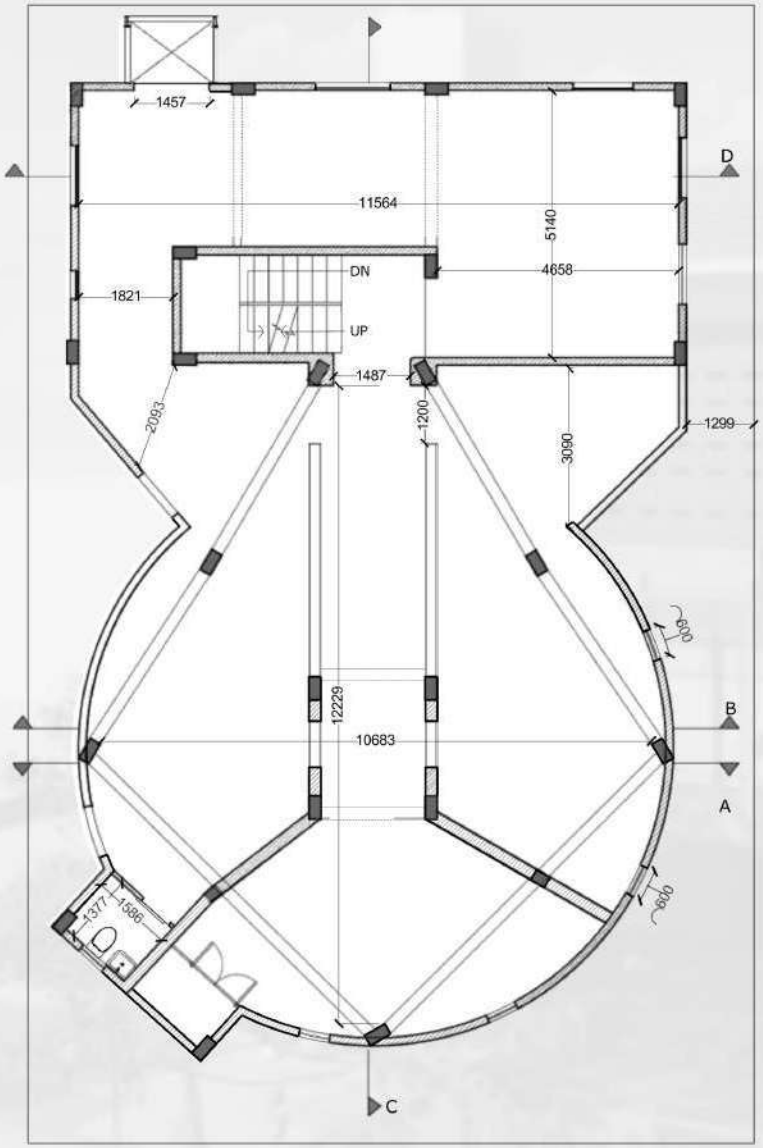

Second floor Plan


Road

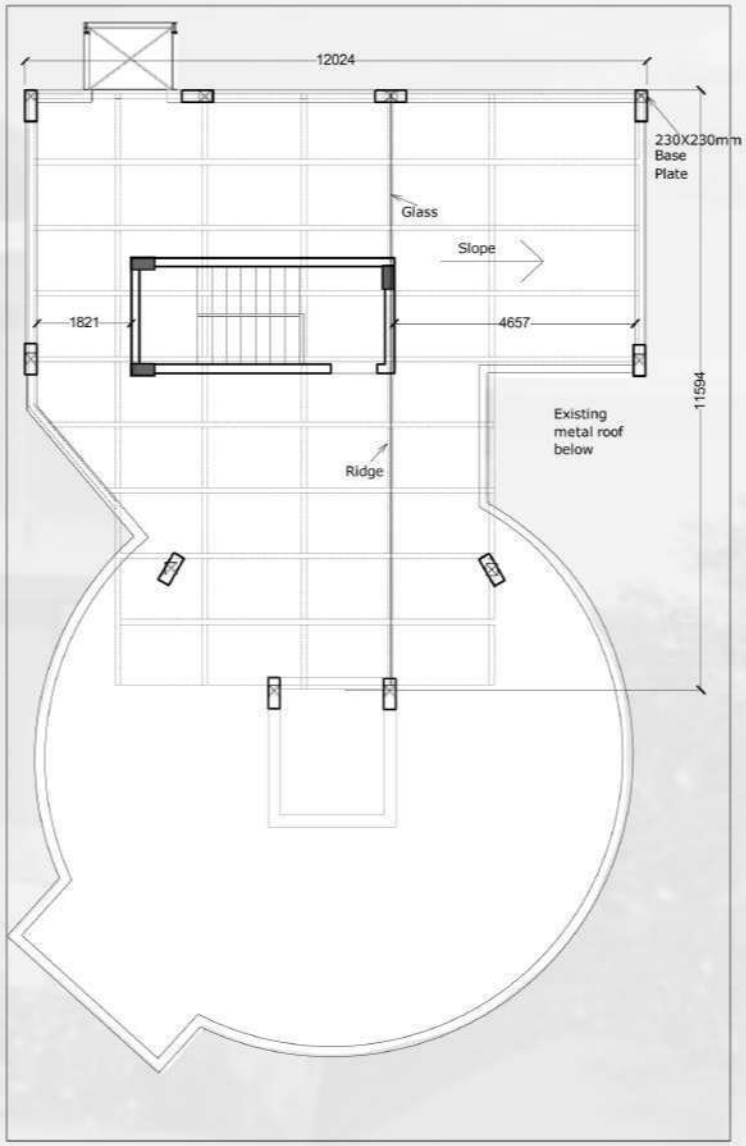


Terrace Plan

Road


-ALL DIMENSIONS ARE IN MM
-ALL DIMENSIONS IN THE DRAWING ARE TO BE READ AND NOT TO BE MEASURED
-THIS DRAWING SHALL SUPERSEDE ITS PREVIOUS REVISIONS.
-ALL DIMENSIONS SHALL BE CO-RELATED WITH STRUCTURAL AND SERVICE DRAWINGS AND ANY AMBIGUITY SHALL BE IMMEDIATELY BROUGHT TO THE NOTICE OF THE ARCHITECT BEFORE THE COMMENCEMENT OF WORK.

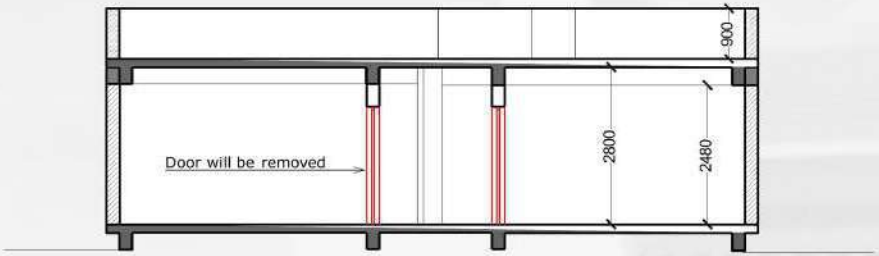


Section A

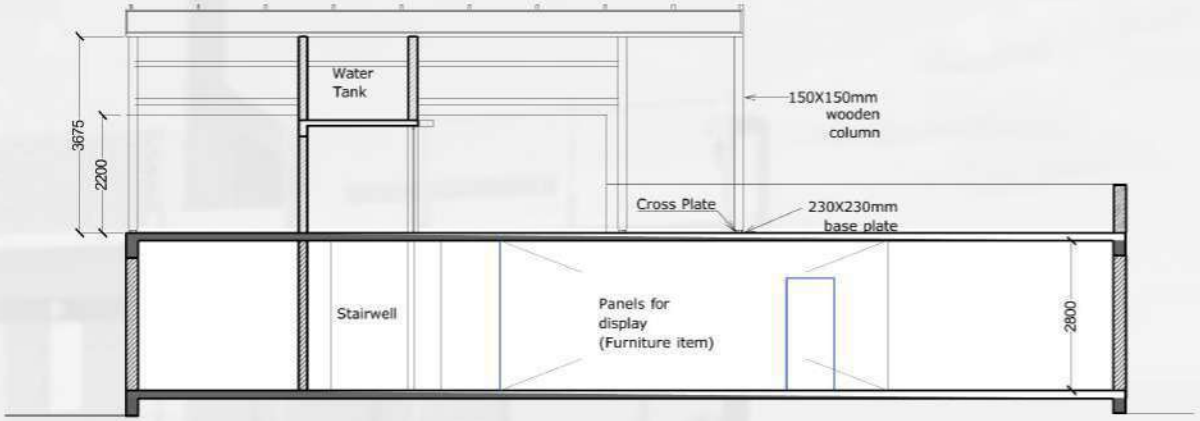

Section C

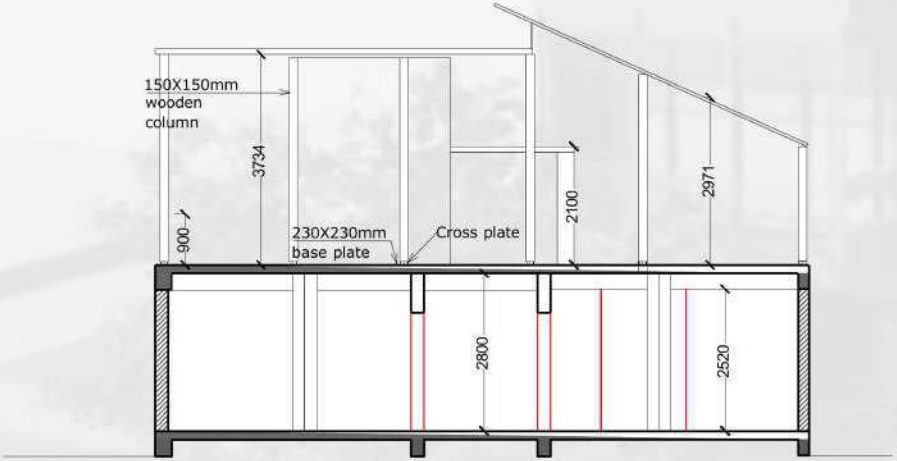



Section B

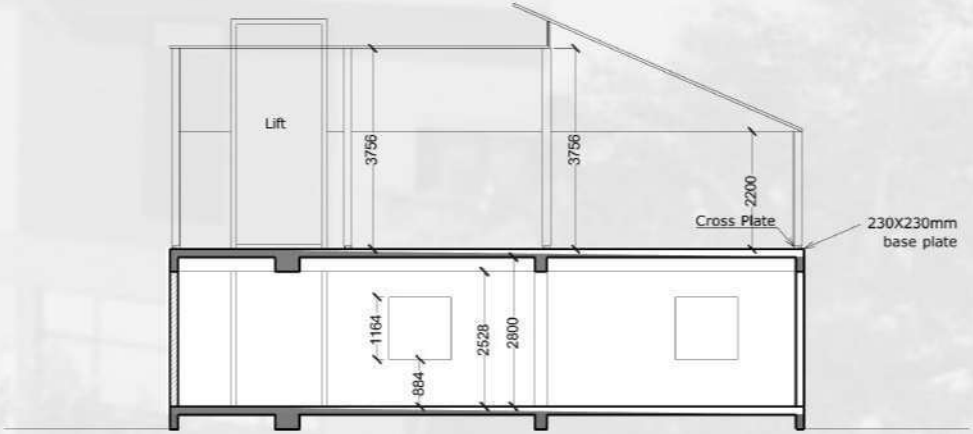


Section D


-ALL DIMENSIONS ARE IN MM
-ALL DIMENSIONS IN THE DRAWING ARE TO BE READ AND NOT TO BE MEASURED
-THIS DRAWING SHALL SUPERSEDE ITS PREVIOUS REVISIONS.
-ALL DIMENSIONS SHALL BE CO-RELATED WITH STRUCTURAL AND SERVICE DRAWINGS AND ANY AMBIGUITY SHALL BE IMMEDIATELY BROUGHT TO THE NOTICE OF THE ARCHITECT BEFORE THE COMMENCEMENT OF WORK.

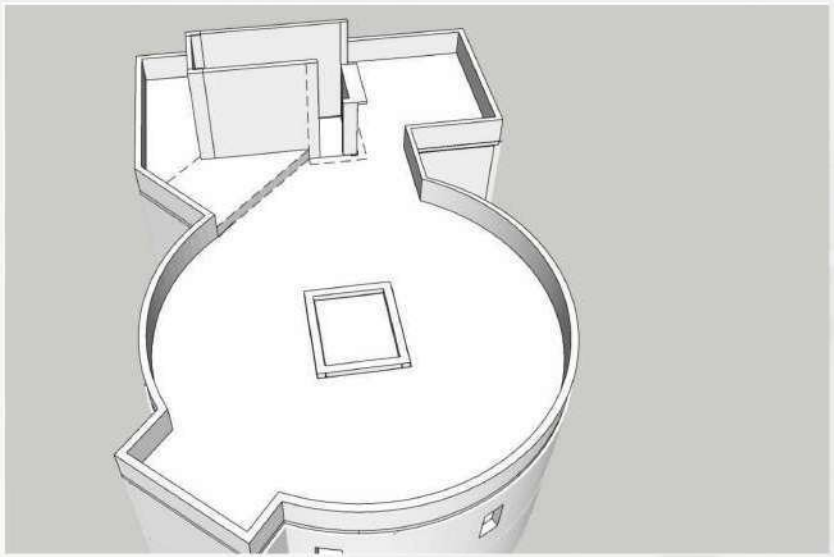

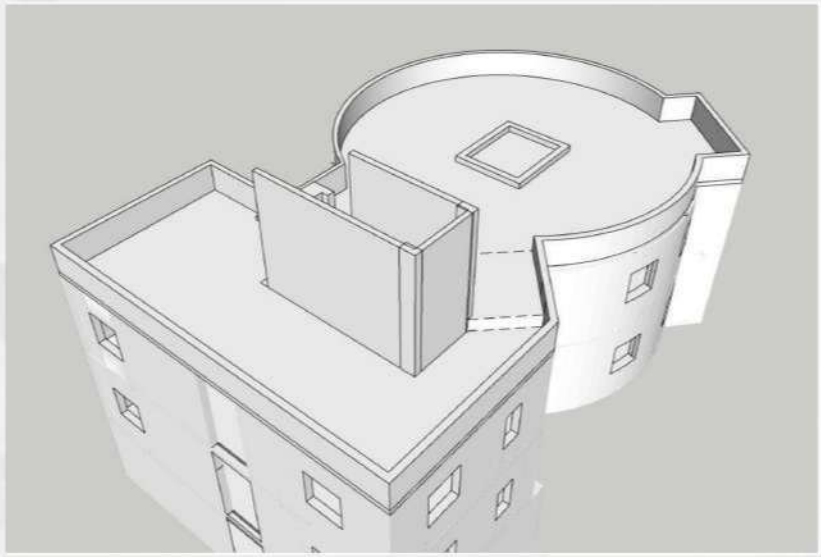

Existing structure

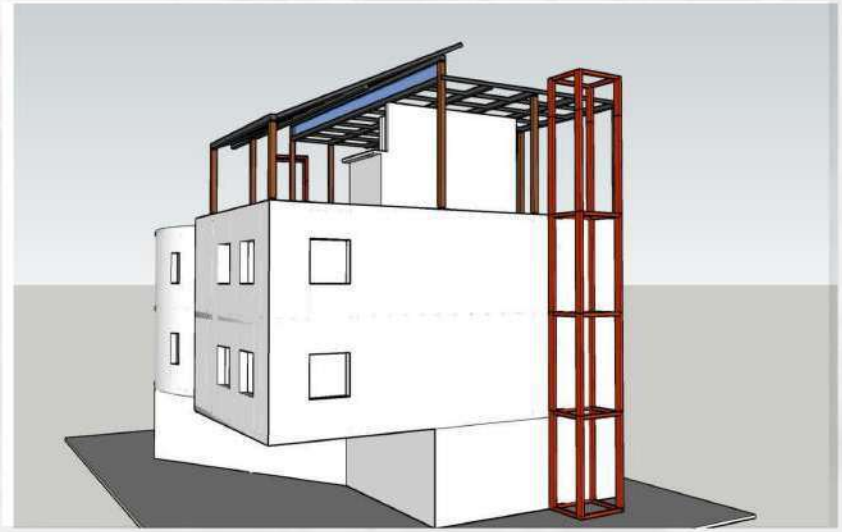


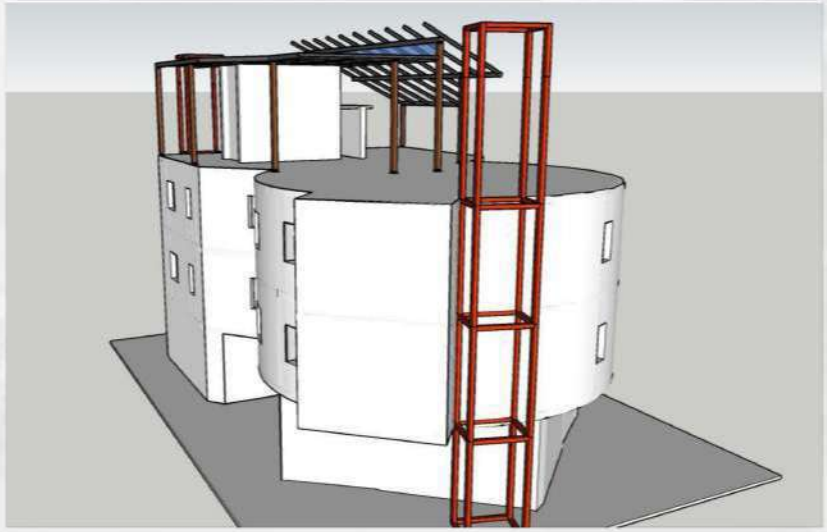


Proposed lift positions

-ALL DIMENSIONS ARE IN MM
-ALL DIMENSIONS IN THE DRAWING ARE TO BE READ AND NOT TO BE MEASURED
-THIS DRAWING SHALL SUPERSEDE ITS PREVIOUS REVISIONS.
-ALL DIMENSIONS SHALL BE CO-RELATED WITH STRUCTURAL AND SERVICE DRAWINGS AND ANY AMBIGUITY SHALL BE IMMEDIATELY BROUGHT TO THE NOTICE OF THE ARCHITECT BEFORE THE COMMENCEMENT OF WORK.


Amravati Plans

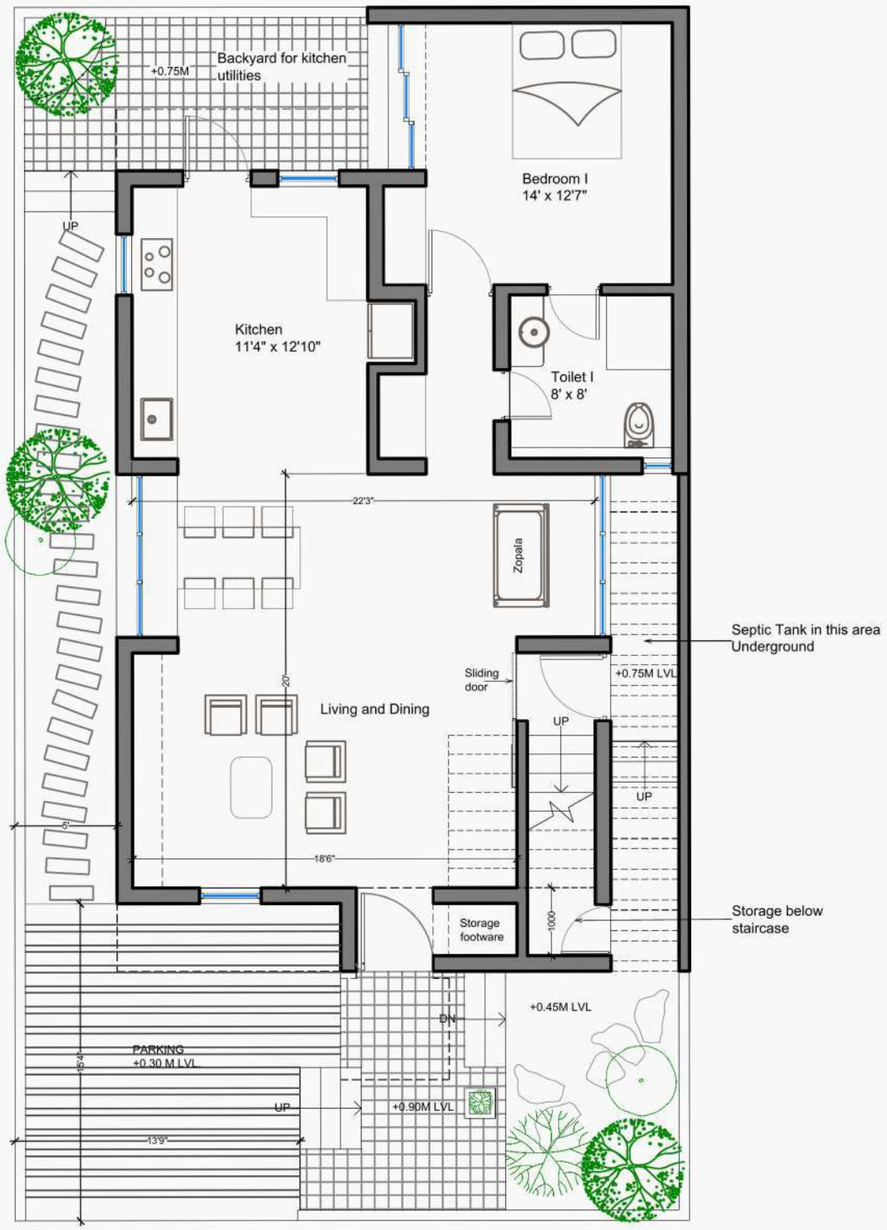

GROUND FLOOR PLAN

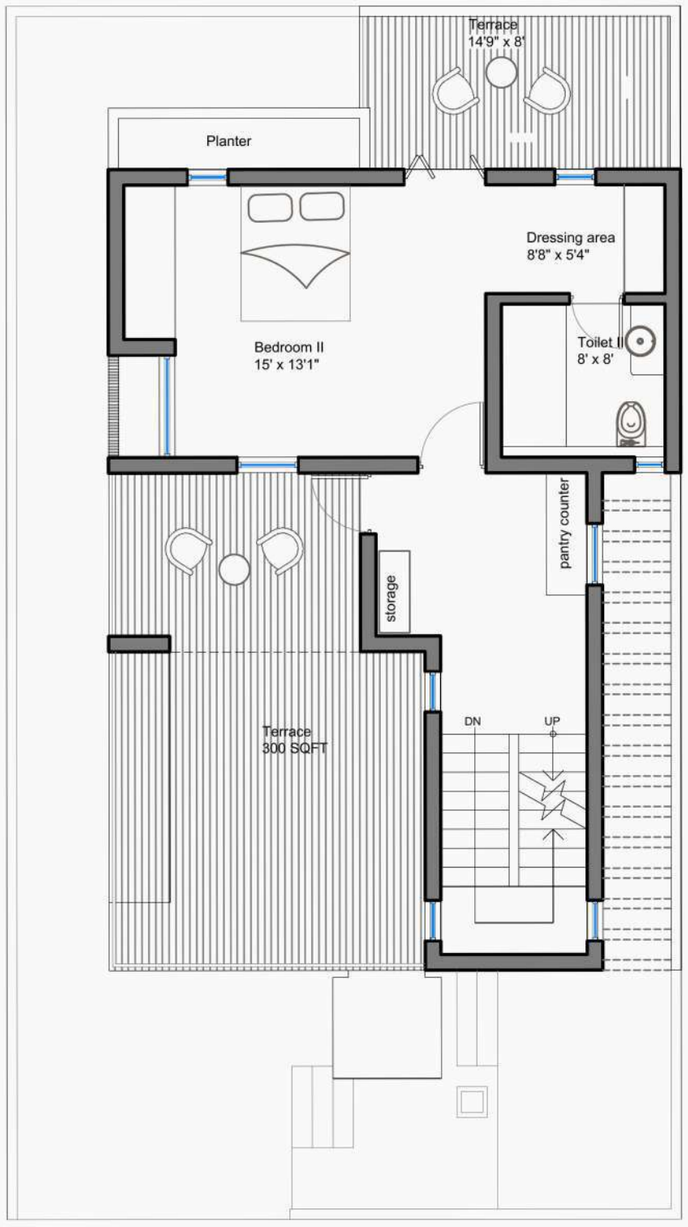


FIRST FLOOR PLAN

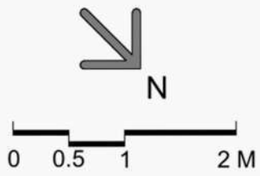


-ALL DIMENSIONS ARE IN MM
-ALL DIMENSIONS IN THE DRAWING ARE TO BE READ AND NOT TO BE MEASURED
-THIS DRAWING SHALL SUPERSEDE ITS PREVIOUS REVISIONS.
-ALL DIMENSIONS SHALL BE CO-RELATED WITH STRUCTURAL AND SERVICE DRAWINGS AND ANY AMBIGUITY SHALL BE IMMEDIATELY BROUGHT TO THE NOTICE OF THE ARCHITECT BEFORE THE COMMENCEMENT OF WORK.


Amravati Plans

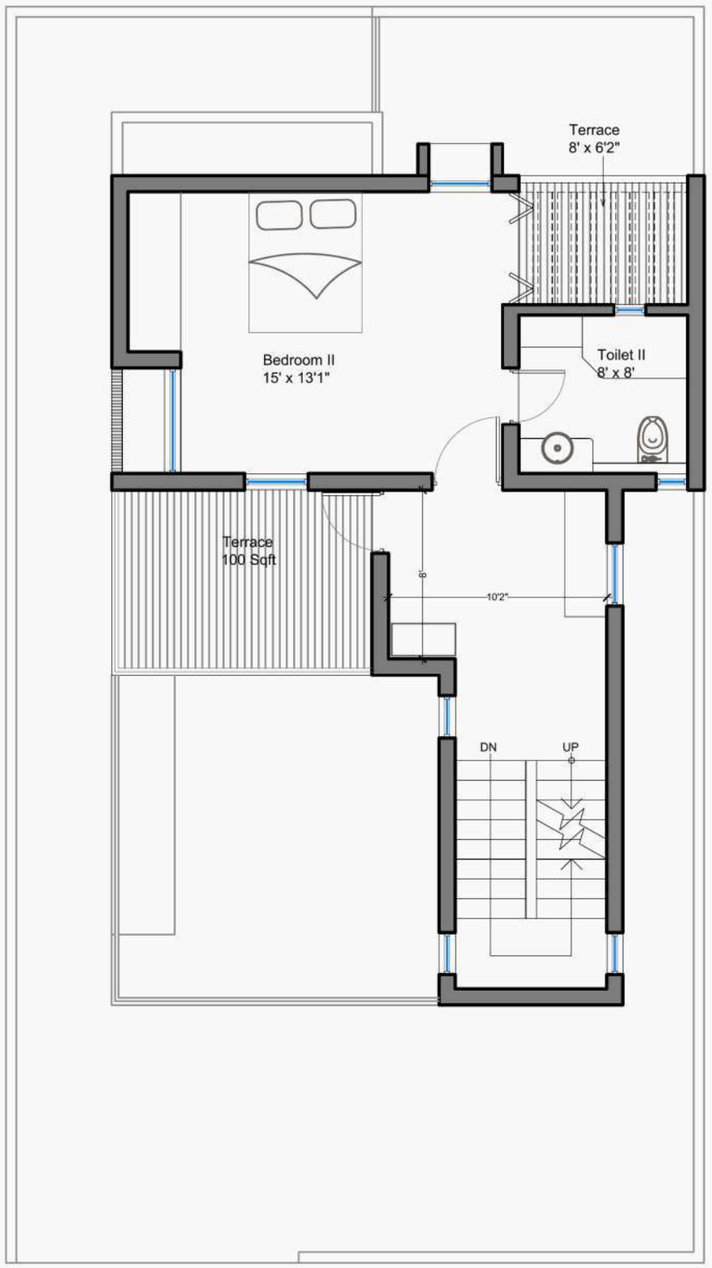

SECOND FLOOR PLAN

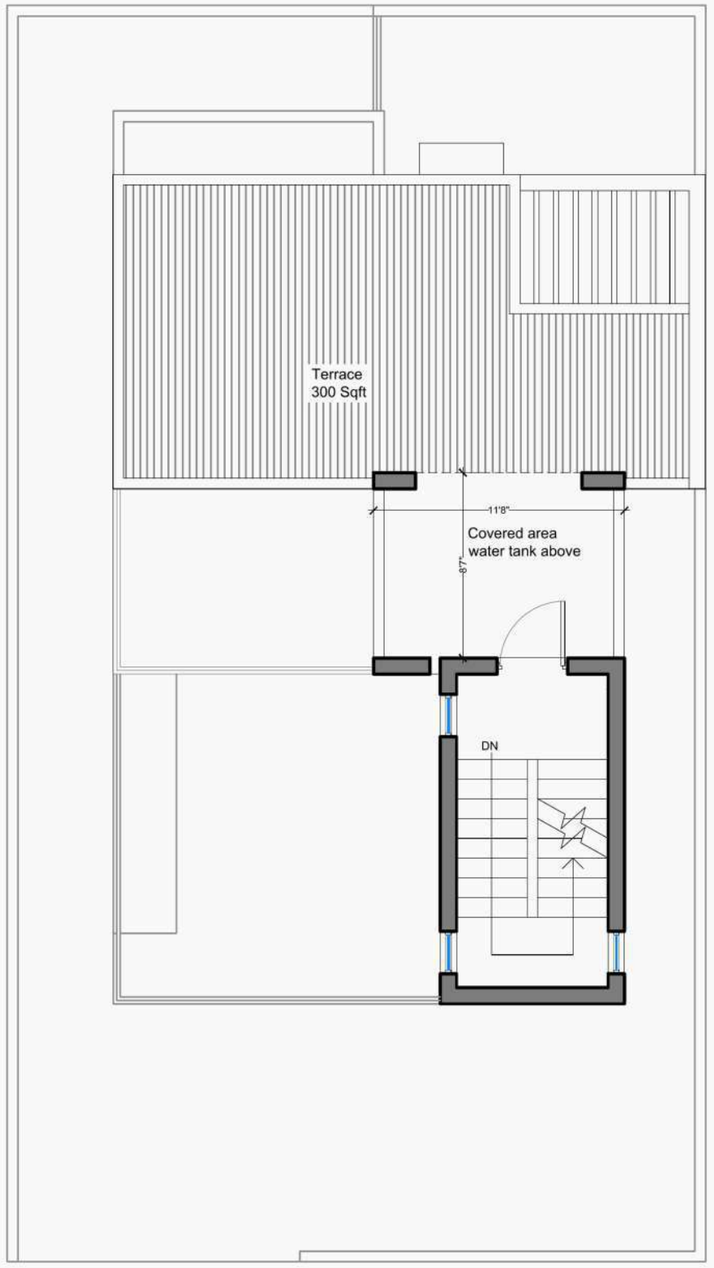

TERRACE FLOOR PLAN

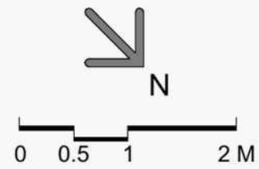

-ALL DIMENSIONS ARE IN MM
-ALL DIMENSIONS IN THE DRAWING ARE TO BE READ AND NOT TO BE MEASURED
-THIS DRAWING SHALL SUPERSEDE ITS PREVIOUS REVISIONS.
-ALL DIMENSIONS SHALL BE CO-RELATED WITH STRUCTURAL AND SERVICE DRAWINGS AND ANY AMBIGUITY SHALL BE IMMEDIATELY BROUGHT TO THE NOTICE OF THE ARCHITECT BEFORE THE COMMENCEMENT OF WORK.

Amravati Bungalow











-ALL DIMENSIONS ARE IN MM
-ALL DIMENSIONS IN THE DRAWING ARE TO BE READ AND NOT TO BE MEASURED
-THIS DRAWING SHALL SUPERSEDE ITS PREVIOUS REVISIONS.
-ALL DIMENSIONS SHALL BE CO-RELATED WITH STRUCTURAL AND SERVICE DRAWINGS AND ANY AMBIGUITY SHALL BE IMMEDIATELY BROUGHT TO THE NOTICE OF THE ARCHITECT BEFORE THE COMMENCEMENT OF WORK.

Krushnakunj Toilet Plan

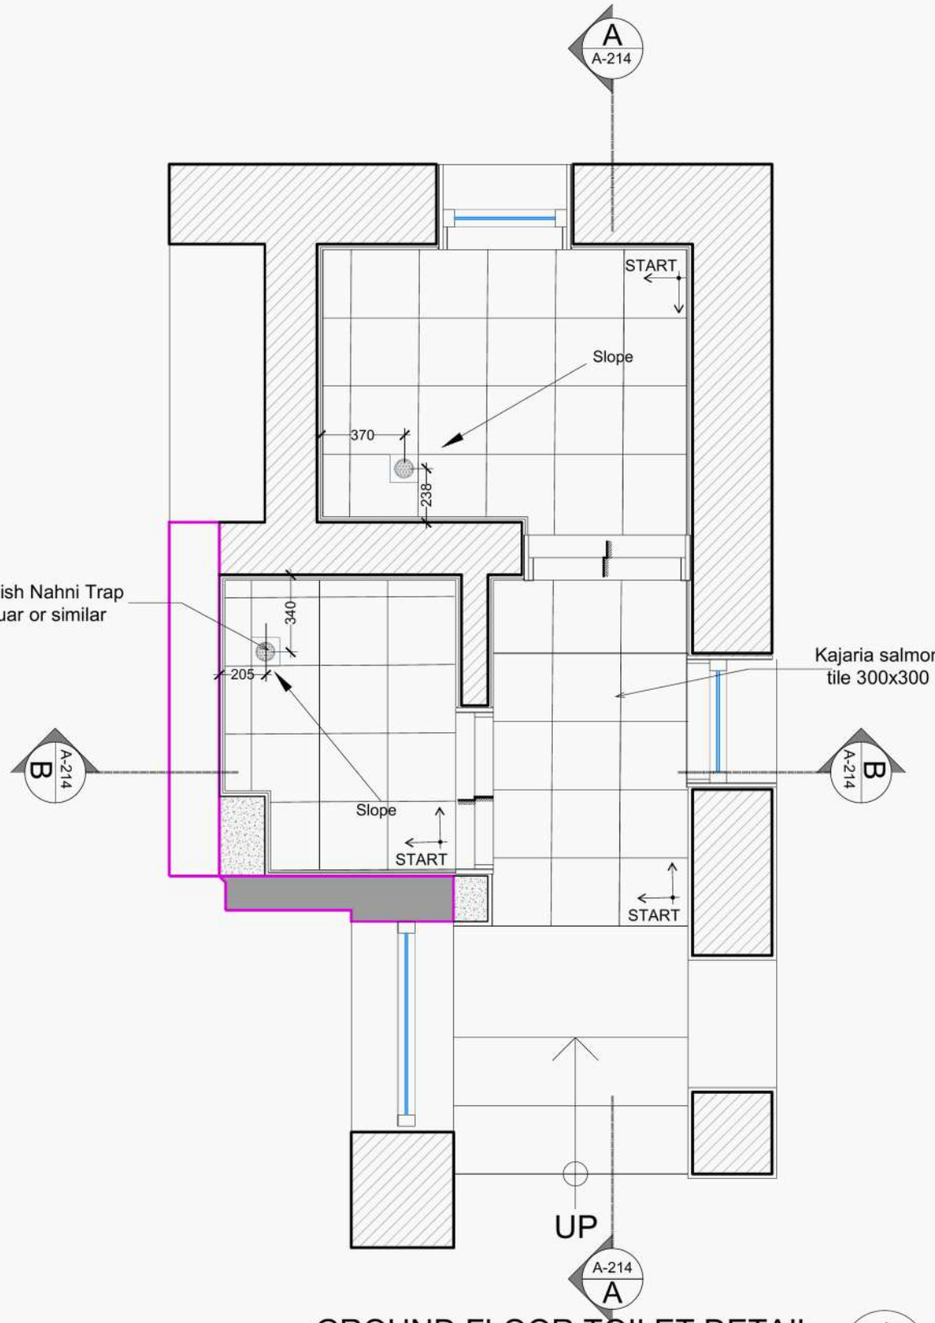


GROUND FLOOR TOILET DETAIL 1 / A-213
1:25

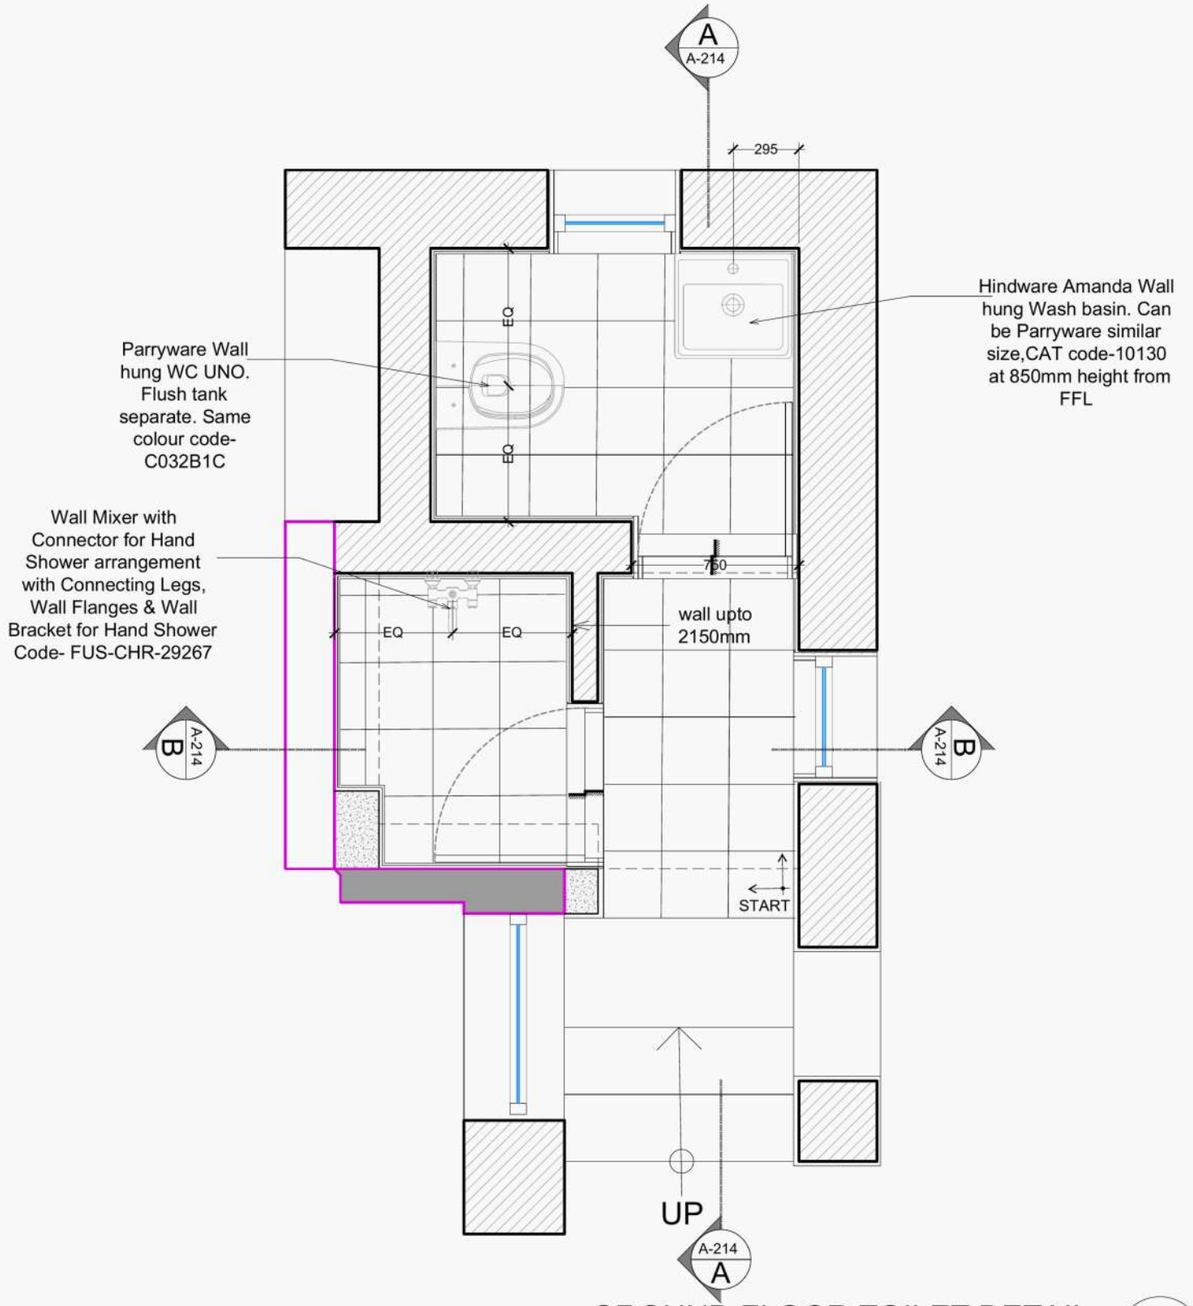


GROUND FLOOR TOILET DETAIL 2 / A-213
1:25

-ALL DIMENSIONS ARE IN MM
-ALL DIMENSIONS IN THE DRAWING ARE TO BE READ AND NOT TO BE MEASURED
-THIS DRAWING SHALL SUPERSEDE ITS PREVIOUS REVISIONS.
-ALL DIMENSIONS SHALL BE CO-RELATED WITH STRUCTURAL AND SERVICE DRAWINGS AND ANY AMBIGUITY SHALL BE IMMEDIATELY BROUGHT TO THE NOTICE OF THE ARCHITECT BEFORE THE COMMENCEMENT OF WORK.

Krushnakunj Sections

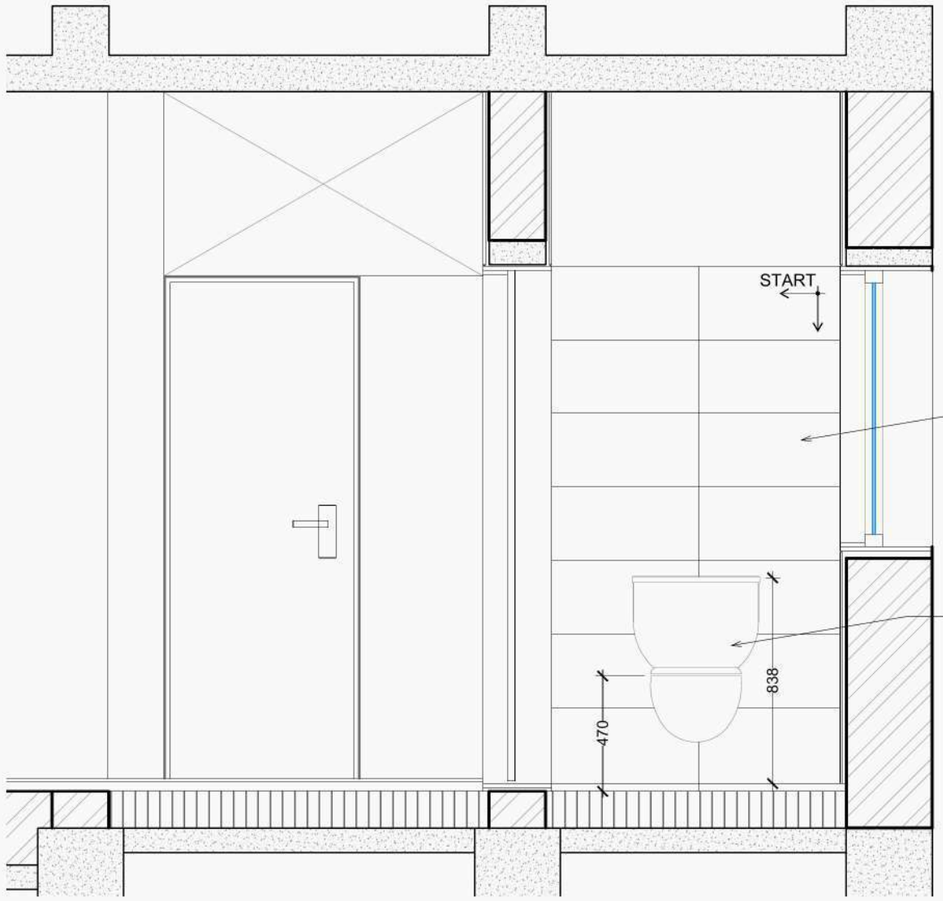


SECTION AA 1
1:25 A-214

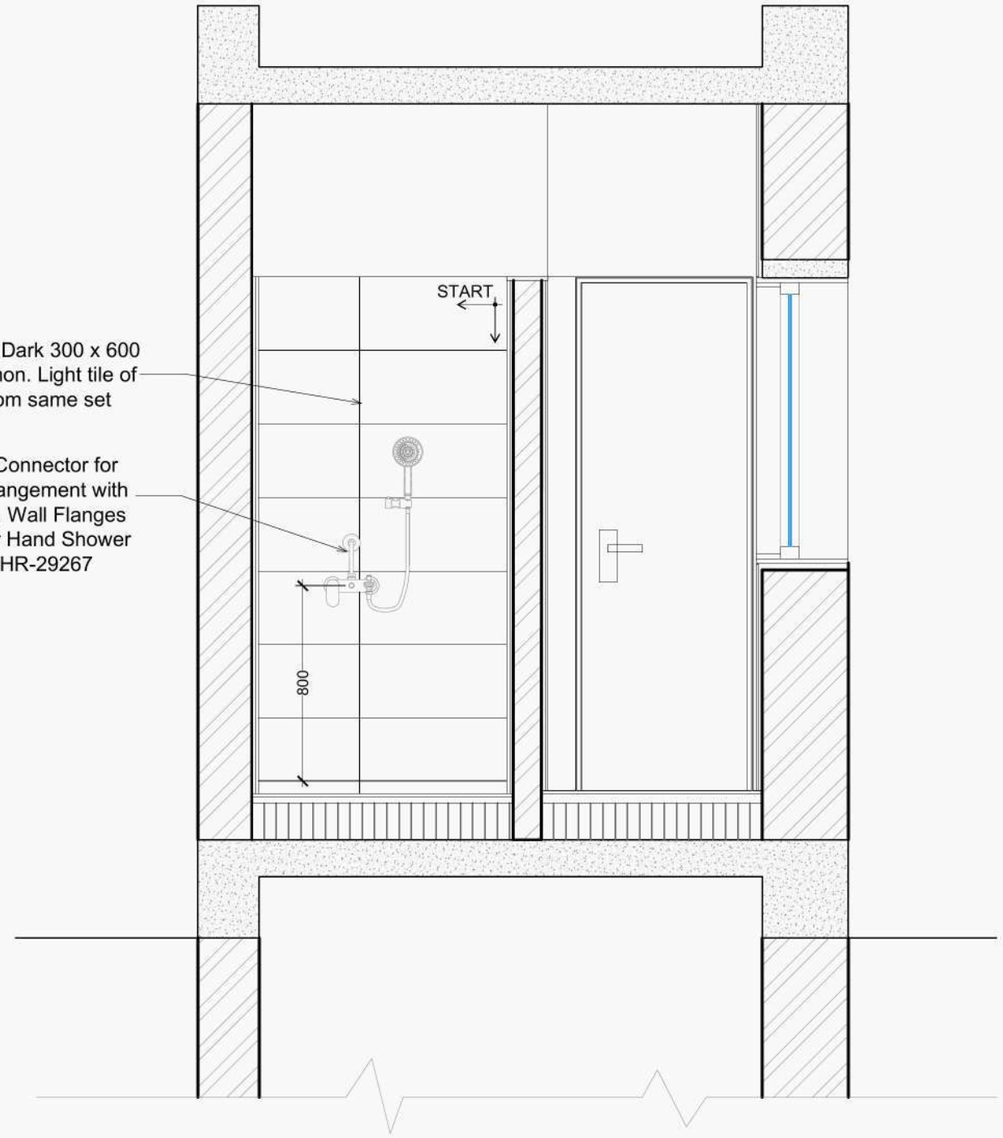


SECTION BB 2
1:25 A-214

-ALL DIMENSIONS ARE IN MM
-ALL DIMENSIONS IN THE DRAWING ARE TO BE READ AND NOT TO BE MEASURED
-THIS DRAWING SHALL SUPERSEDE ITS PREVIOUS REVISIONS.
-ALL DIMENSIONS SHALL BE CO-RELATED WITH STRUCTURAL AND SERVICE DRAWINGS AND ANY AMBIGUITY SHALL BE IMMEDIATELY BROUGHT TO THE NOTICE OF THE ARCHITECT BEFORE THE COMMENCEMENT OF WORK.


Balcony Detail

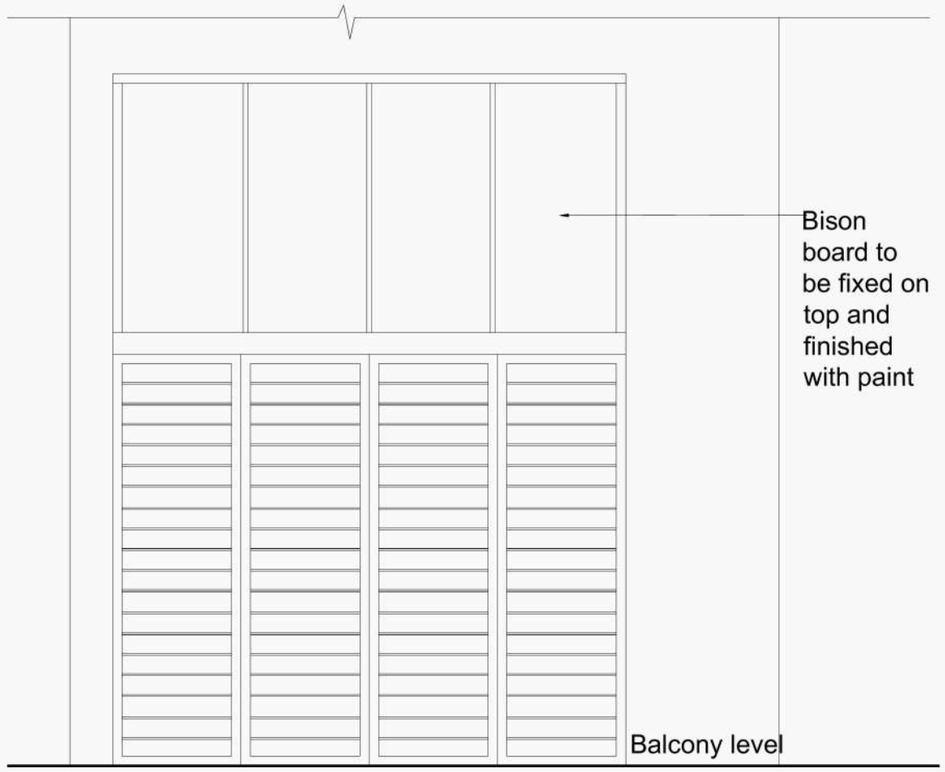


Elevation from Garden side

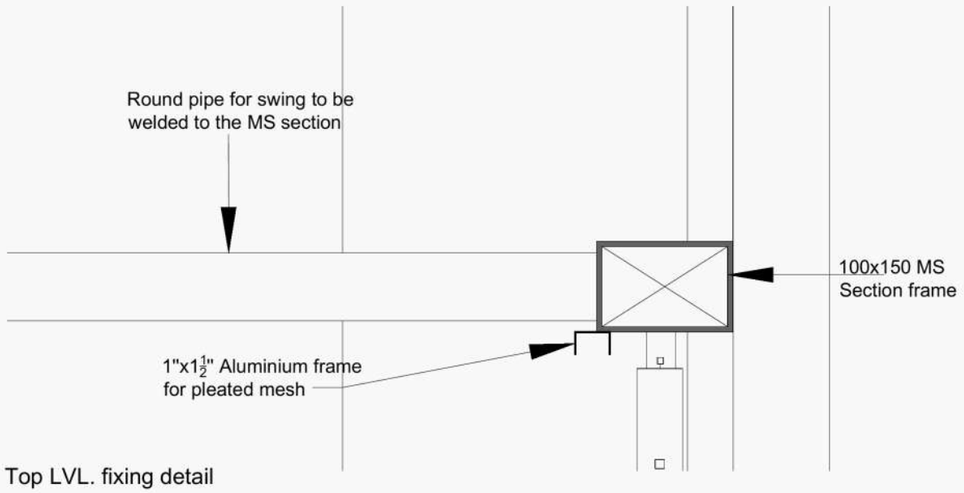

Top LVL. fixing detail

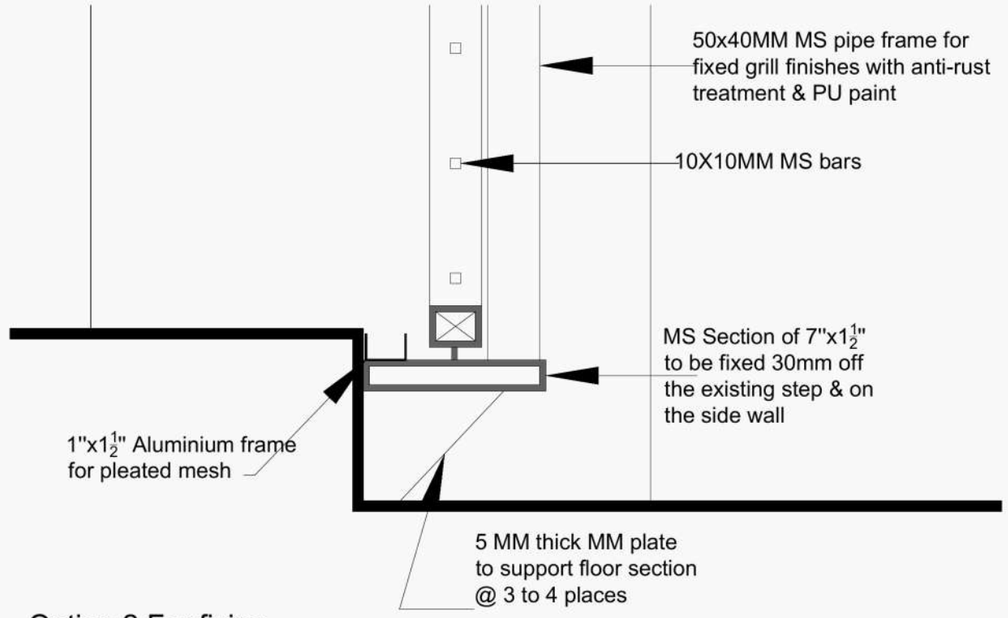

Option 2 For fixing at Bottom LVL.

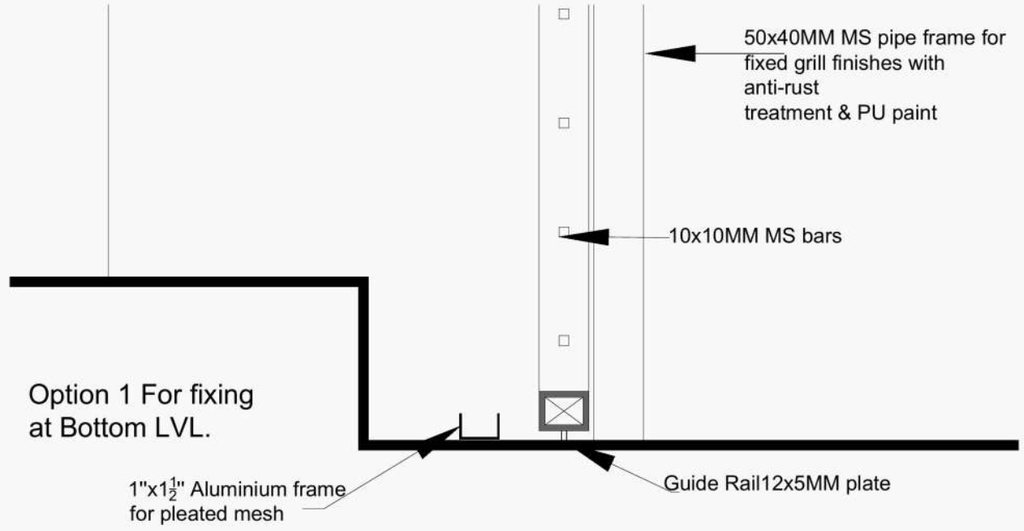


Option 1 For fixing at Bottom LVL.

Balcony MS Grill door details

-ALL DIMENSIONS ARE IN MM
-ALL DIMENSIONS IN THE DRAWING ARE TO BE READ AND NOT TO BE MEASURED
-THIS DRAWING SHALL SUPERSEDE ITS PREVIOUS REVISIONS.
-ALL DIMENSIONS SHALL BE CO-RELATED WITH STRUCTURAL AND SERVICE DRAWINGS AND ANY AMBIGUITY SHALL BE IMMEDIATELY BROUGHT TO THE NOTICE OF THE ARCHITECT BEFORE THE COMMENCEMENT OF WORK.

Kitchen Renovation Project



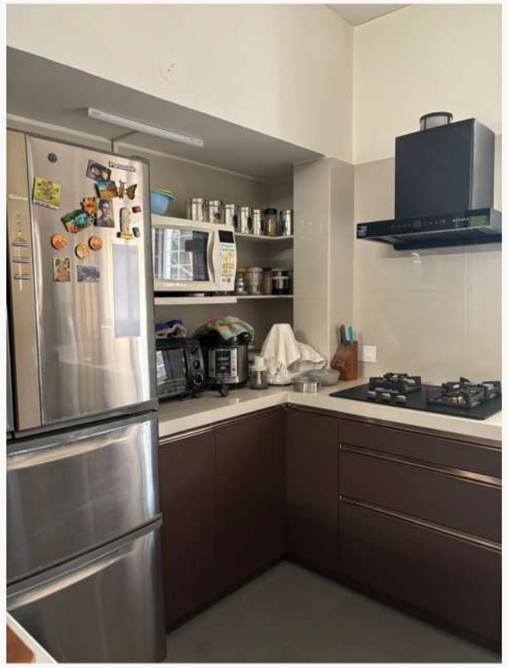







-ALL DIMENSIONS ARE IN MM
-ALL DIMENSIONS IN THE DRAWING ARE TO BE READ AND NOT TO BE MEASURED
-THIS DRAWING SHALL SUPERSEDE ITS PREVIOUS REVISIONS.
-ALL DIMENSIONS SHALL BE CO-RELATED WITH STRUCTURAL AND SERVICE DRAWINGS AND ANY AMBIGUITY SHALL BE IMMEDIATELY BROUGHT TO THE NOTICE OF THE ARCHITECT BEFORE THE COMMENCEMENT OF WORK.

Swan lake Apartment Toilet Detail

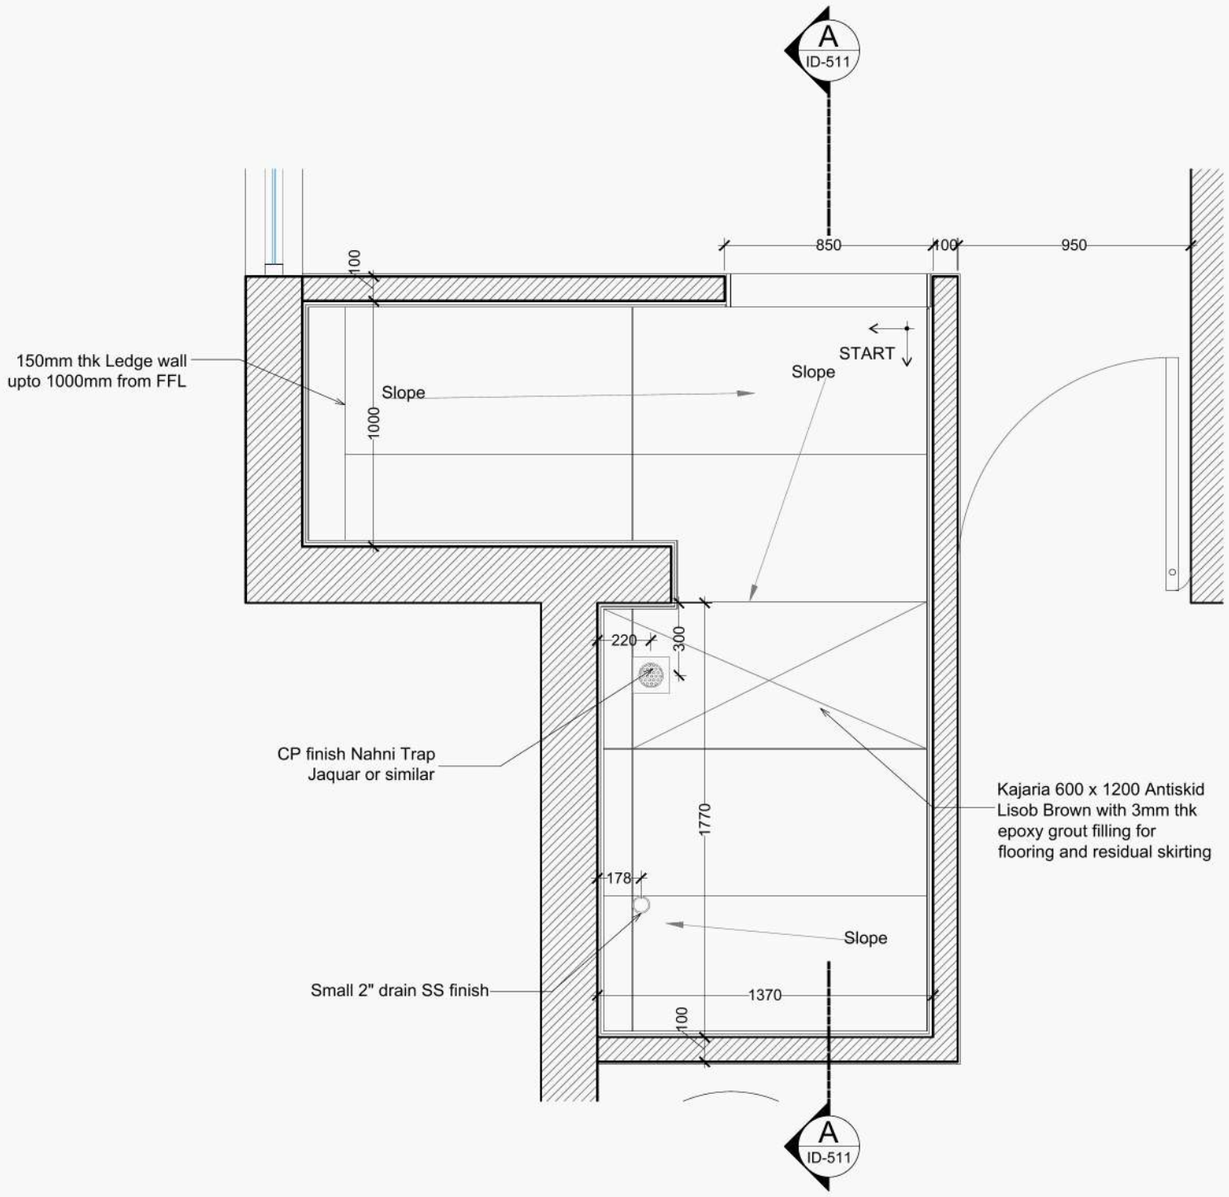


FLOOR PLAN 1
1:25
ID-510

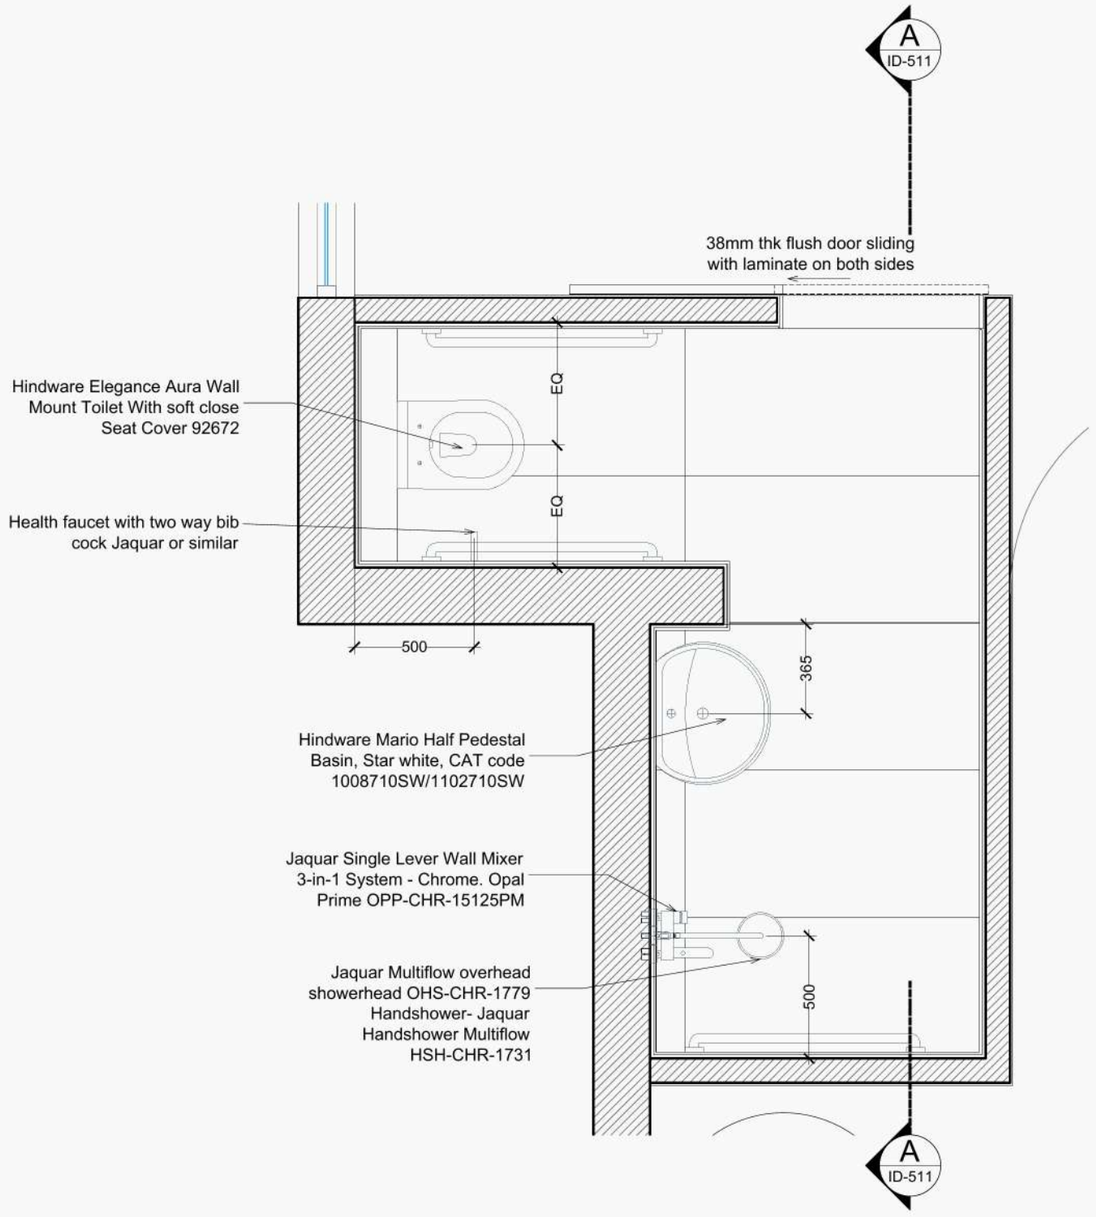

TOILET PLAN 2
1:25
ID-510

-ALL DIMENSIONS ARE IN MM
-ALL DIMENSIONS IN THE DRAWING ARE TO BE READ AND NOT TO BE MEASURED
-THIS DRAWING SHALL SUPERSEDE ITS PREVIOUS REVISIONS.
-ALL DIMENSIONS SHALL BE CO-RELATED WITH STRUCTURAL AND SERVICE DRAWINGS AND ANY AMBIGUITY SHALL BE IMMEDIATELY BROUGHT TO THE NOTICE OF THE ARCHITECT BEFORE THE COMMENCEMENT OF WORK.

Swan lake Apartment Toilet section

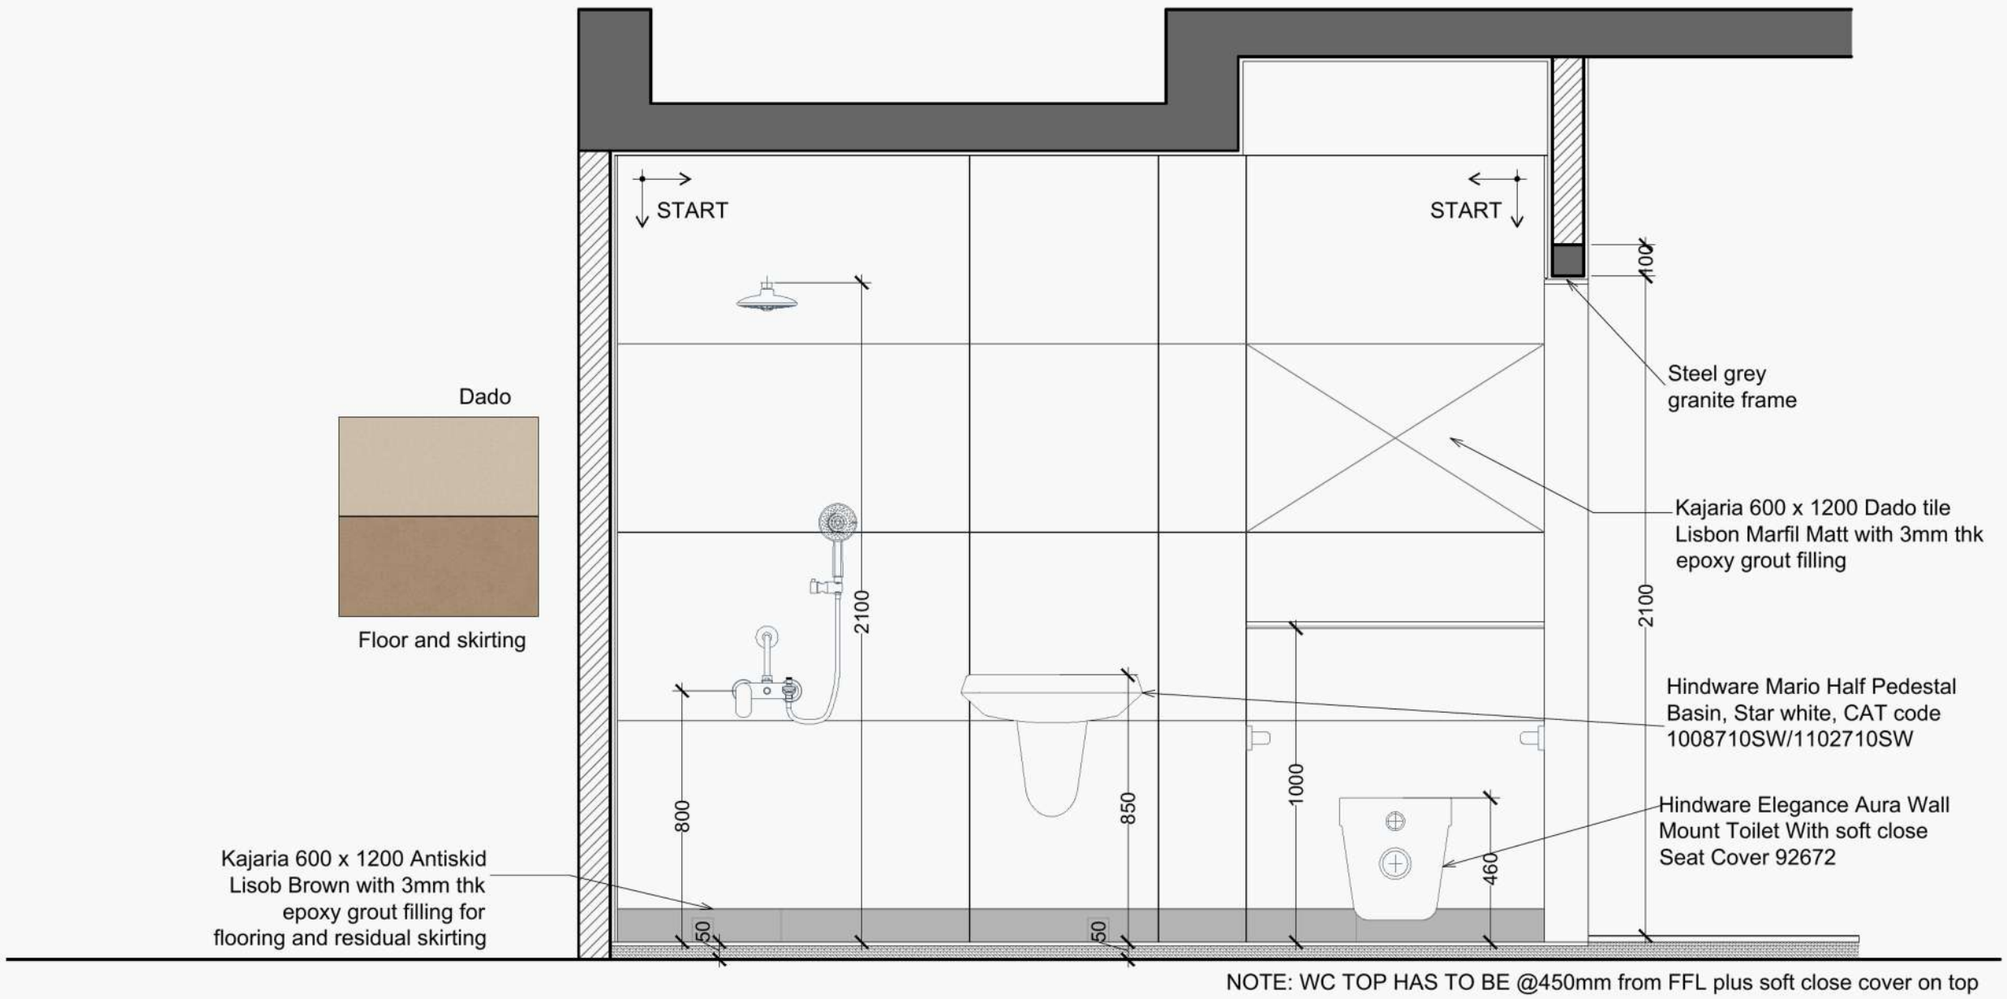

NOTE: WC TOP HAS TO BE @450mm from FFL plus soft close cover on top

SECTION A

1:25

1
ID-511


-ALL DIMENSIONS ARE IN MM
-ALL DIMENSIONS IN THE DRAWING ARE TO BE READ AND NOT TO BE MEASURED
-THIS DRAWING SHALL SUPERSEDE ITS PREVIOUS REVISIONS.
-ALL DIMENSIONS SHALL BE CO-RELATED WITH STRUCTURAL AND SERVICE DRAWINGS AND ANY AMBIGUITY SHALL BE IMMEDIATELY BROUGHT TO THE NOTICE OF THE ARCHITECT BEFORE THE COMMENCEMENT OF WORK.

Flat Renovation









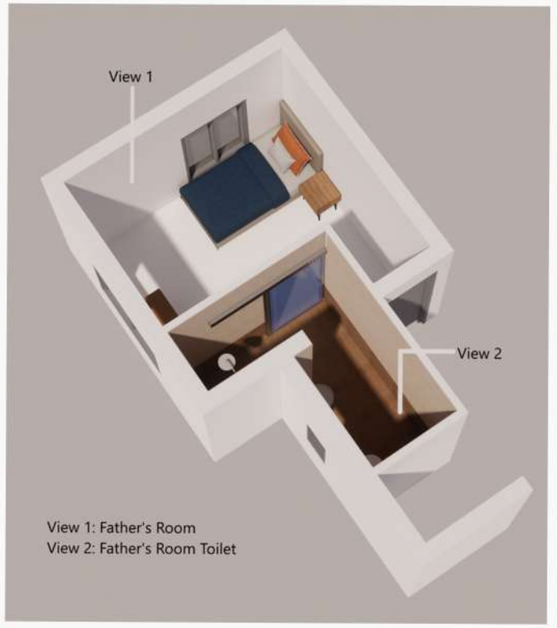


-ALL DIMENSIONS ARE IN MM
-ALL DIMENSIONS IN THE DRAWING ARE TO BE READ AND NOT TO BE MEASURED
-THIS DRAWING SHALL SUPERSEDE ITS PREVIOUS REVISIONS.
-ALL DIMENSIONS SHALL BE CO-RELATED WITH STRUCTURAL AND SERVICE DRAWINGS AND ANY AMBIGUITY SHALL BE IMMEDIATELY BROUGHT TO THE NOTICE OF THE ARCHITECT BEFORE THE COMMENCEMENT OF WORK.

Swan Lake Apartment plan & Section

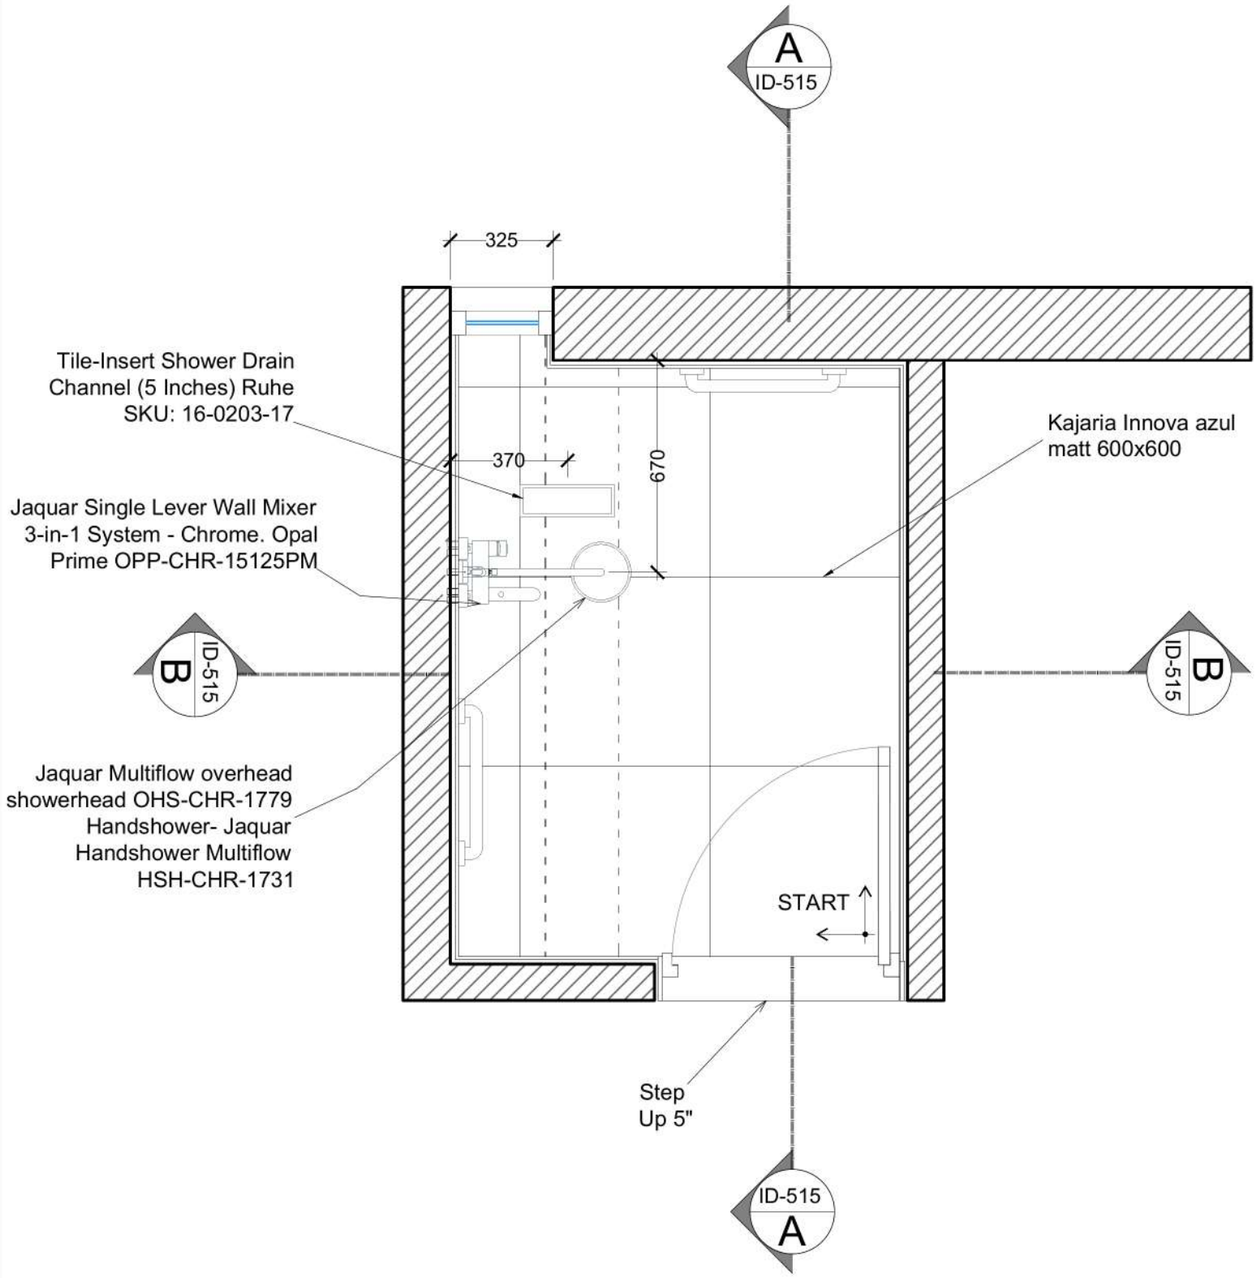

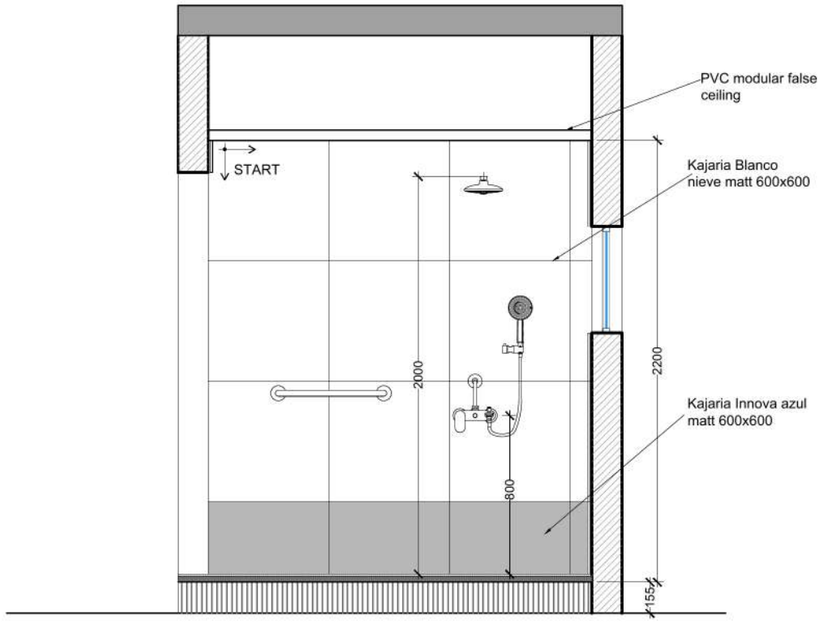


SECTION A

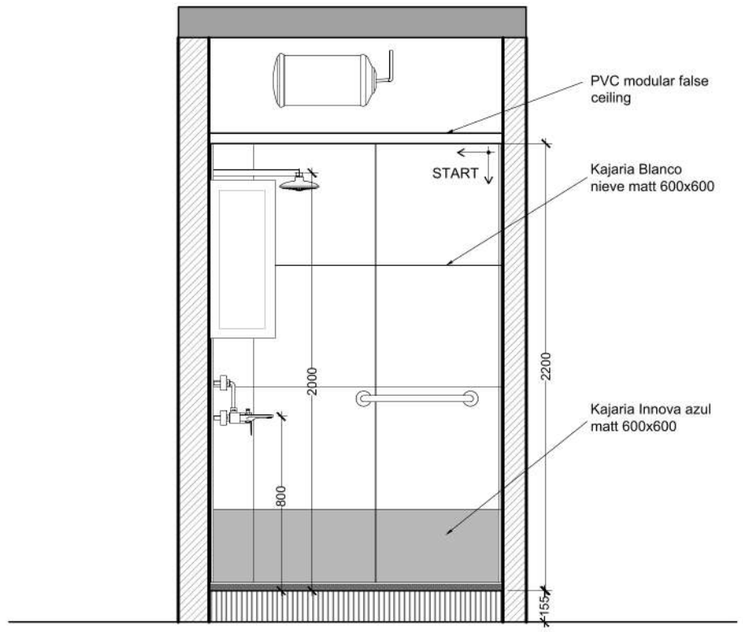

SECTION B

-ALL
-ALL
-THIS DRAWING SHALL SUPERSEDE ITS PREVIOUS REVISIONS.
-ALL DIMENSIONS SHALL BE CO-RELATED WITH STRUCTURAL AND SERVICE DRAWINGS AND ANY AMBIGUITY SHALL BE IMMEDIATELY BROUGHT TO THE NOTICE OF THE ARCHITECT BEFORE THE COMMENCEMENT OF WORK.

Swan Lake Apartment Electrical layout

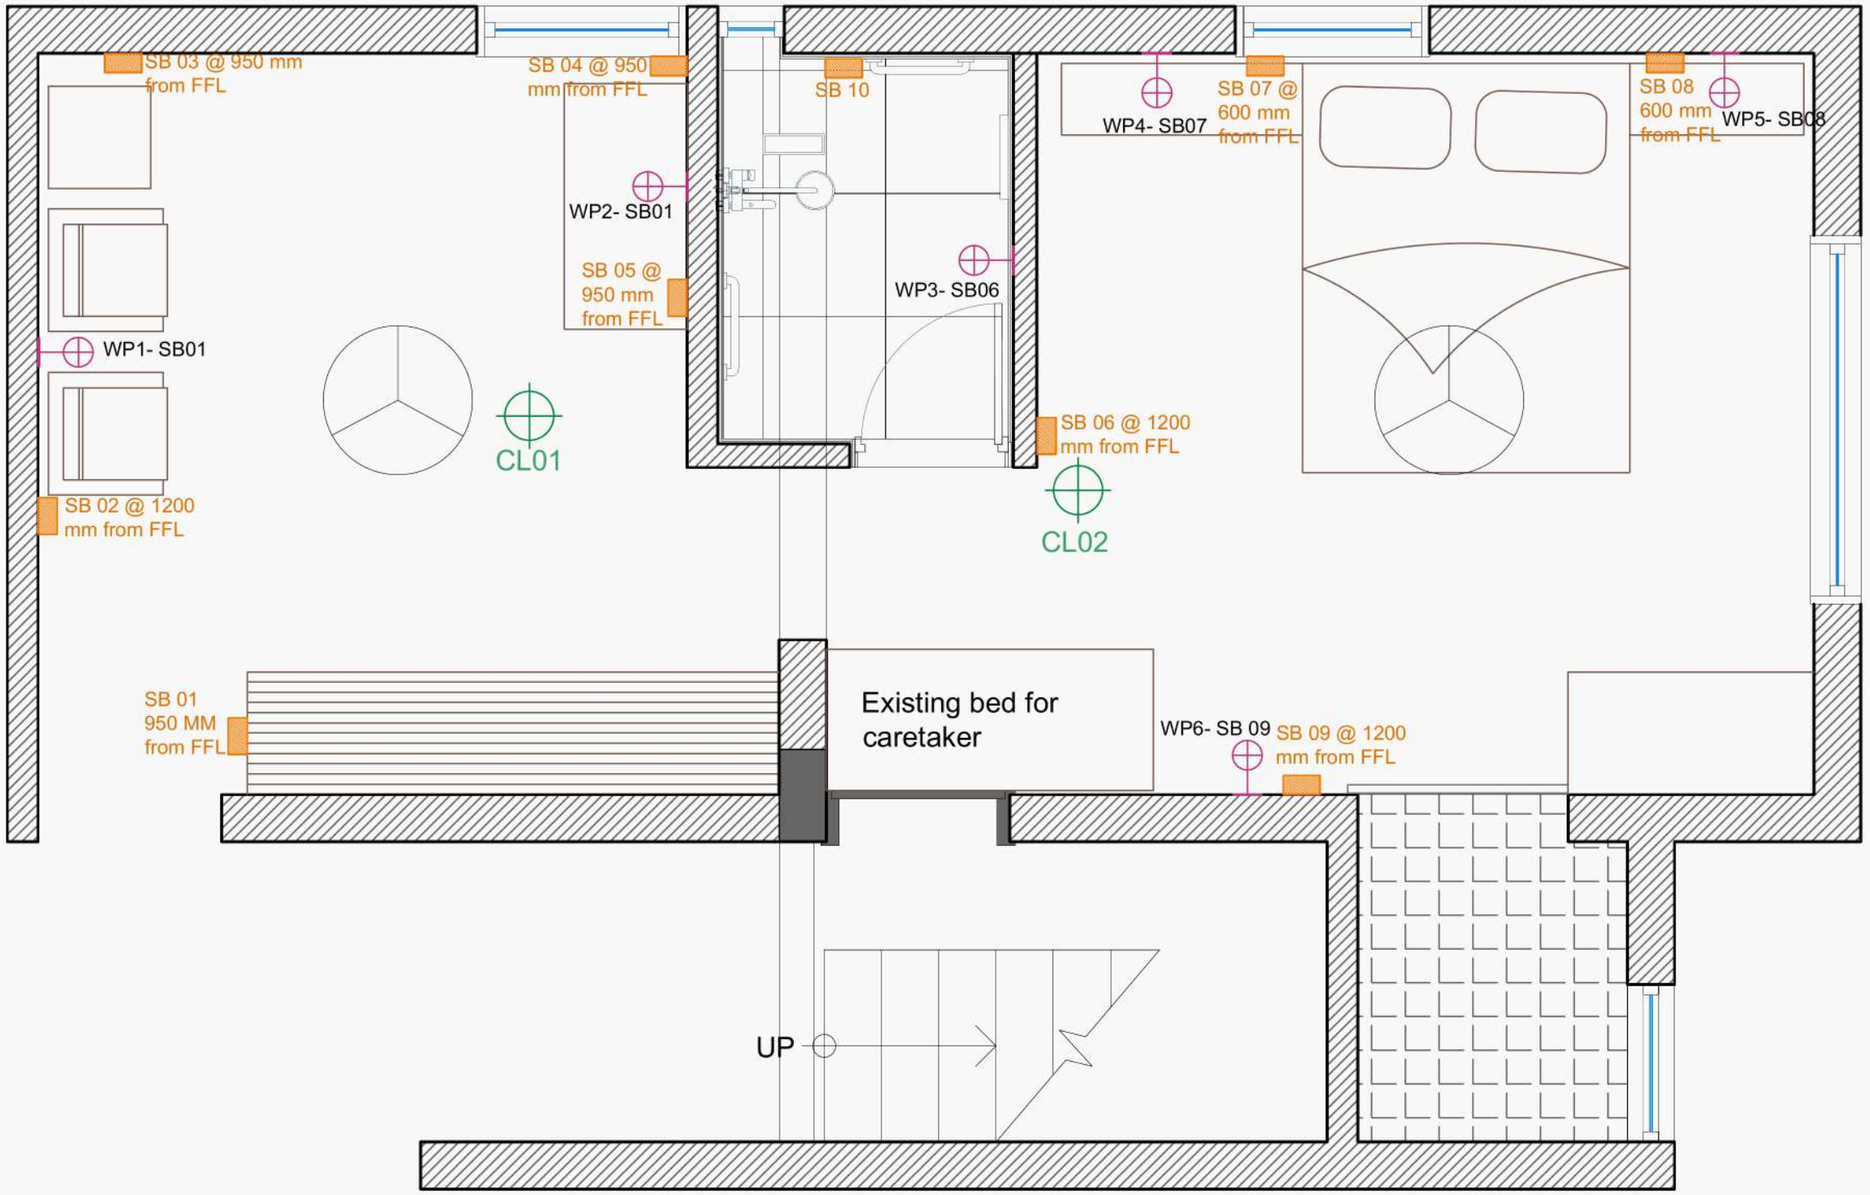

SB 01
- Wall points WP1 and WP2
- Fan 1

SB02
- switch socket

SB 03
- Wall Points WP1 and WP2(two way)
- Switch socket

SB 04 and **SB 05**
- Switch socket

SB 06
- Wall point WP 3
- Water heater control switch

SB 07 and **SB 08**
- Wall point WP 4 and WP 5(Two way with SB 07 AND SB 08)
- Switch socket and Fan 2

SB 09
- Wall point WP 06


SB 10
- Water heater 15amp socket

CL - Ceiling Light

-ALL DIMENSIONS ARE IN MM
-ALL DIMENSIONS IN THE DRAWING ARE TO BE READ AND NOT TO BE MEASURED
-THIS DRAWING SHALL SUPERSEDE ITS PREVIOUS REVISIONS.
-ALL DIMENSIONS SHALL BE CO-RELATED WITH STRUCTURAL AND SERVICE DRAWINGS AND ANY AMBIGUITY SHALL BE IMMEDIATELY BROUGHT TO THE NOTICE OF THE ARCHITECT BEFORE THE COMMENCEMENT OF WORK.

Flat Renovation



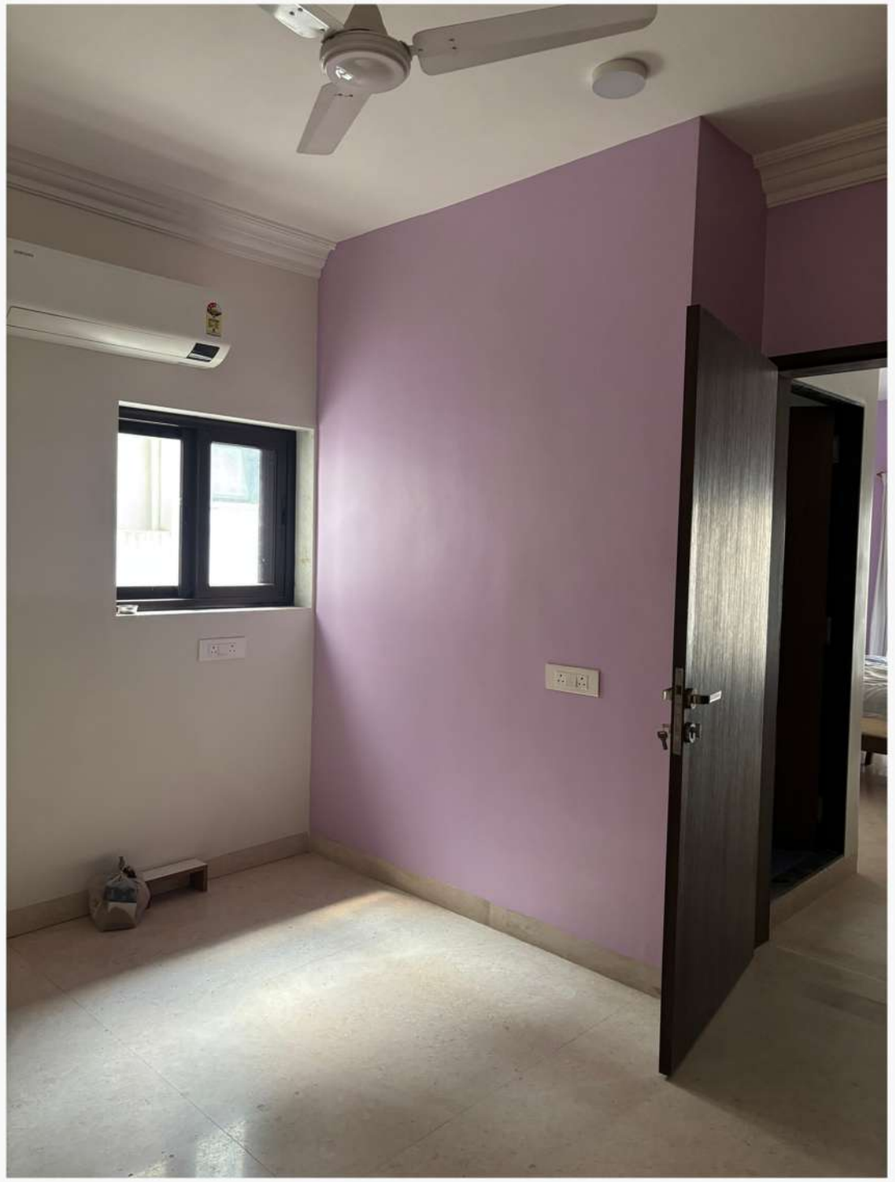

-ALL DIMENSIONS ARE IN MM
-ALL DIMENSIONS IN THE DRAWING ARE TO BE READ AND NOT TO BE MEASURED
-THIS DRAWING SHALL SUPERSEDE ITS PREVIOUS REVISIONS.
-ALL DIMENSIONS SHALL BE CO-RELATED WITH STRUCTURAL AND SERVICE DRAWINGS AND ANY AMBIGUITY SHALL BE IMMEDIATELY BROUGHT TO THE NOTICE OF THE ARCHITECT BEFORE THE COMMENCEMENT OF WORK.